


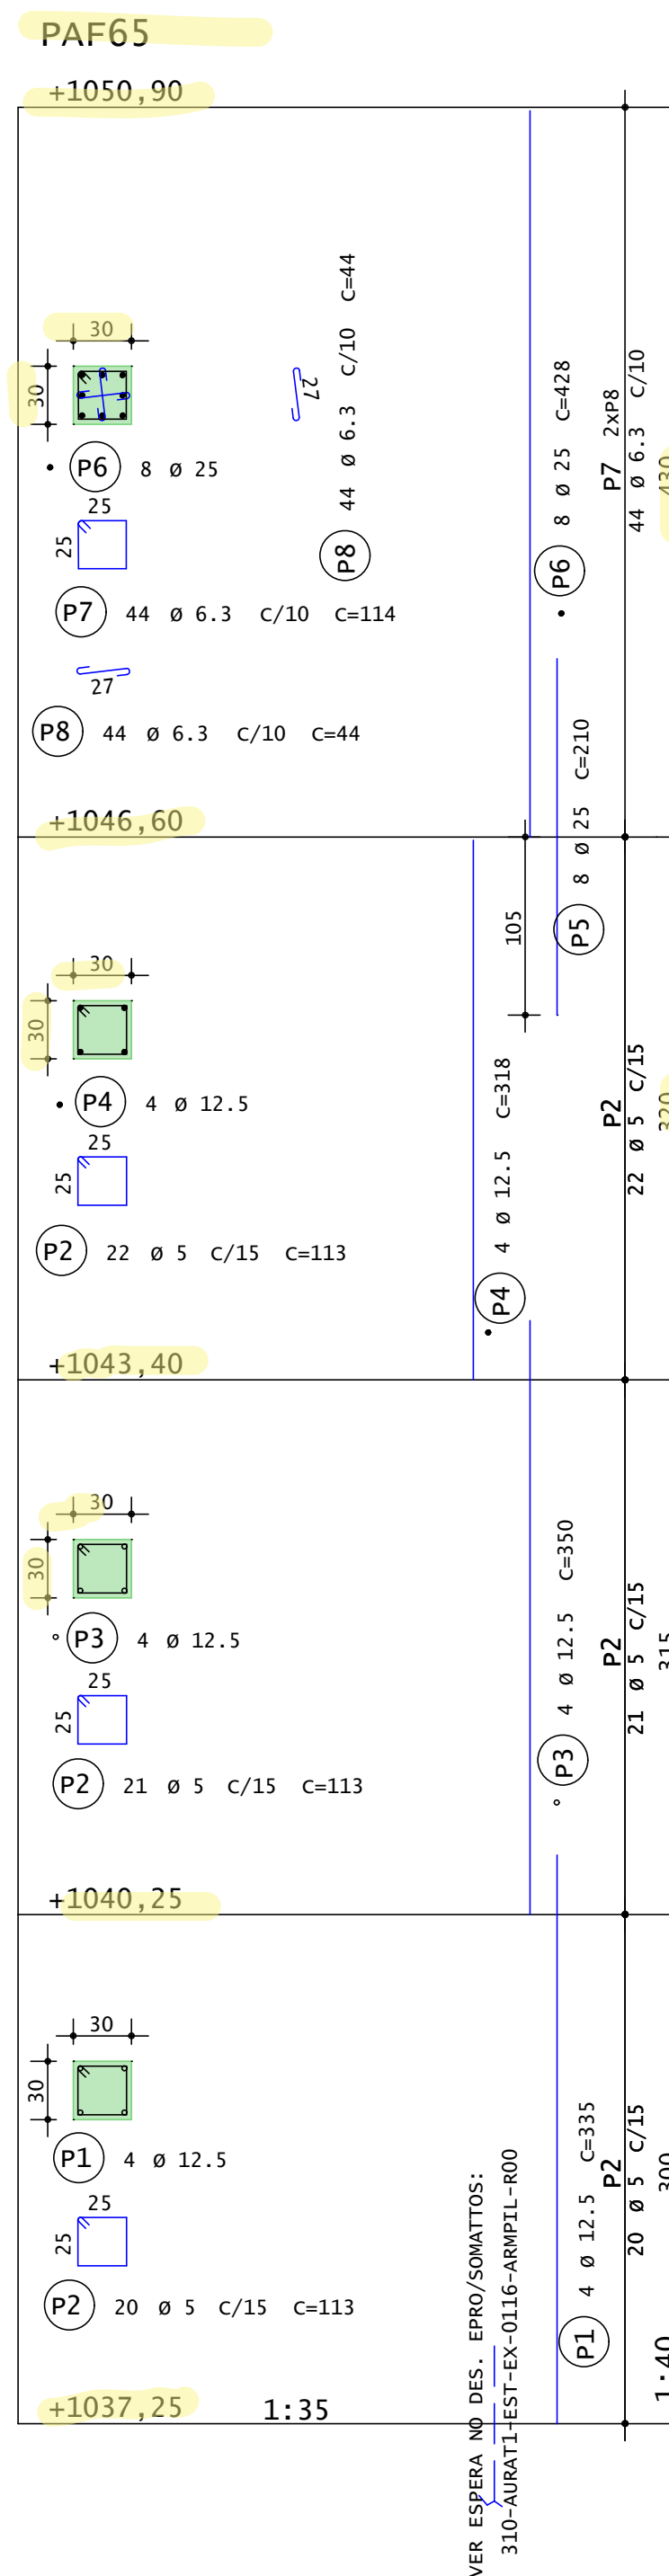

RESUMO ACO CA 50-60				
ACO	BIT (mm)	COMPR (m)	PESO (kg)	
60	5	384	59	
50	6,3	282	69	
50	8	89	35	
50	12,5	224	216	
50	16	81	127	
50	20	43	106	
50	25	193	75	
50	32	40	240	
Peso Total		60 =	59 kgf	
Peso Total		50 =	1549 kgf	

- 1- COTAS EM CENTÍMETRO, NÍVEIS EM METRO;
- 2- CONCRETO ESTRUTURAL:
 - FCK $\geq$ 40,0 MPa;
 - FATOR AGUA/CEMENTO (A/C) $\leq$ 0,60
 - CONSUMO MÍNIMO DE CIMENTO = 280 kg/m³;
 - TEMPO DE CURA, CONFORME CONDIÇÕES CLIMÁTICAS, MÍNIMO DE 7 (SETE) DIAS;
- 3- MÓDULO DE ELASTICIDADE INICIAL DO CONCRETO NBR 6118/2023;
$$E_{ci} = 56000 \sqrt{FCK} \text{ (DADOS EM MPa)} - \alpha(E=1,0 \text{ PARA GRANITO E GNAISSE};$$

PARA FCK $\geq$ 40,0 MPa - $E_{ci} = 33130$ MPa;
- 4- COBRIMENTO = 2,5 cm;
- 5- AÇOS CA 50 e CA 60;

	PROPRIETÁRIO: SOMATTOS PATRIM Q.04 EMPREEND.IMOBILIÁRIOS SPE LTDA CNPJ: 42.306.807/0001-05 AUTOR DO PROJETO: TORRES MIRANDA ARQUITETURA E CONSULTORIA LTDA CAU: 8447-6 RESPONSÁVEL TÉCNICO EXECUÇÃO: BERNARDO IMPELLIZZIERI SÁ MATTOS CREA: 82679/D MG
 Rua Luis Coelho 43, cj. 5º andar - BH - MG Fone: (31)3241-4331 e-mail: epro@epro.com.br	RESPONSÁVEL TÉCNICO PROJ. EXECUTIVO: EPRO ENGENHARIA DE PROJETOS E CONSULTORIA S/C LTDA CREA: 6154/MG ENGENHEIRO COLABORADOR: LUIZ RENATO DE LIMA CREA: 26927/D

EMPRESAMENTO:		310 - AURA - TORRE 1	
CÓDIGO:			
LOCAL:		BAIRRO:	
RUA CEL. GABRIEL FELIPE FARIA, VILA DA SERRA - NOVA LIMA - MG		JARDINAVES	
PROJETO:		DATA 1a. EMISSÃO:	
PROJETO EXECUTIVO ESTRUTURAL		13/10/2025	
		REVISÃO:	
		R00	
CONTEÚDO:		ESCALA:	
ARMAÇÃO DOS PILARES DA ÁREA FRONTAL (TORRE 1) - 4a. PARTE PAF59, PAF62, PAF63, PAF64 e PAF65		INDICADA	
ARQUIVO:		FOLHA:	
310-AURAT1-EST-EX-0133-ARMPIL-R00		133/	