


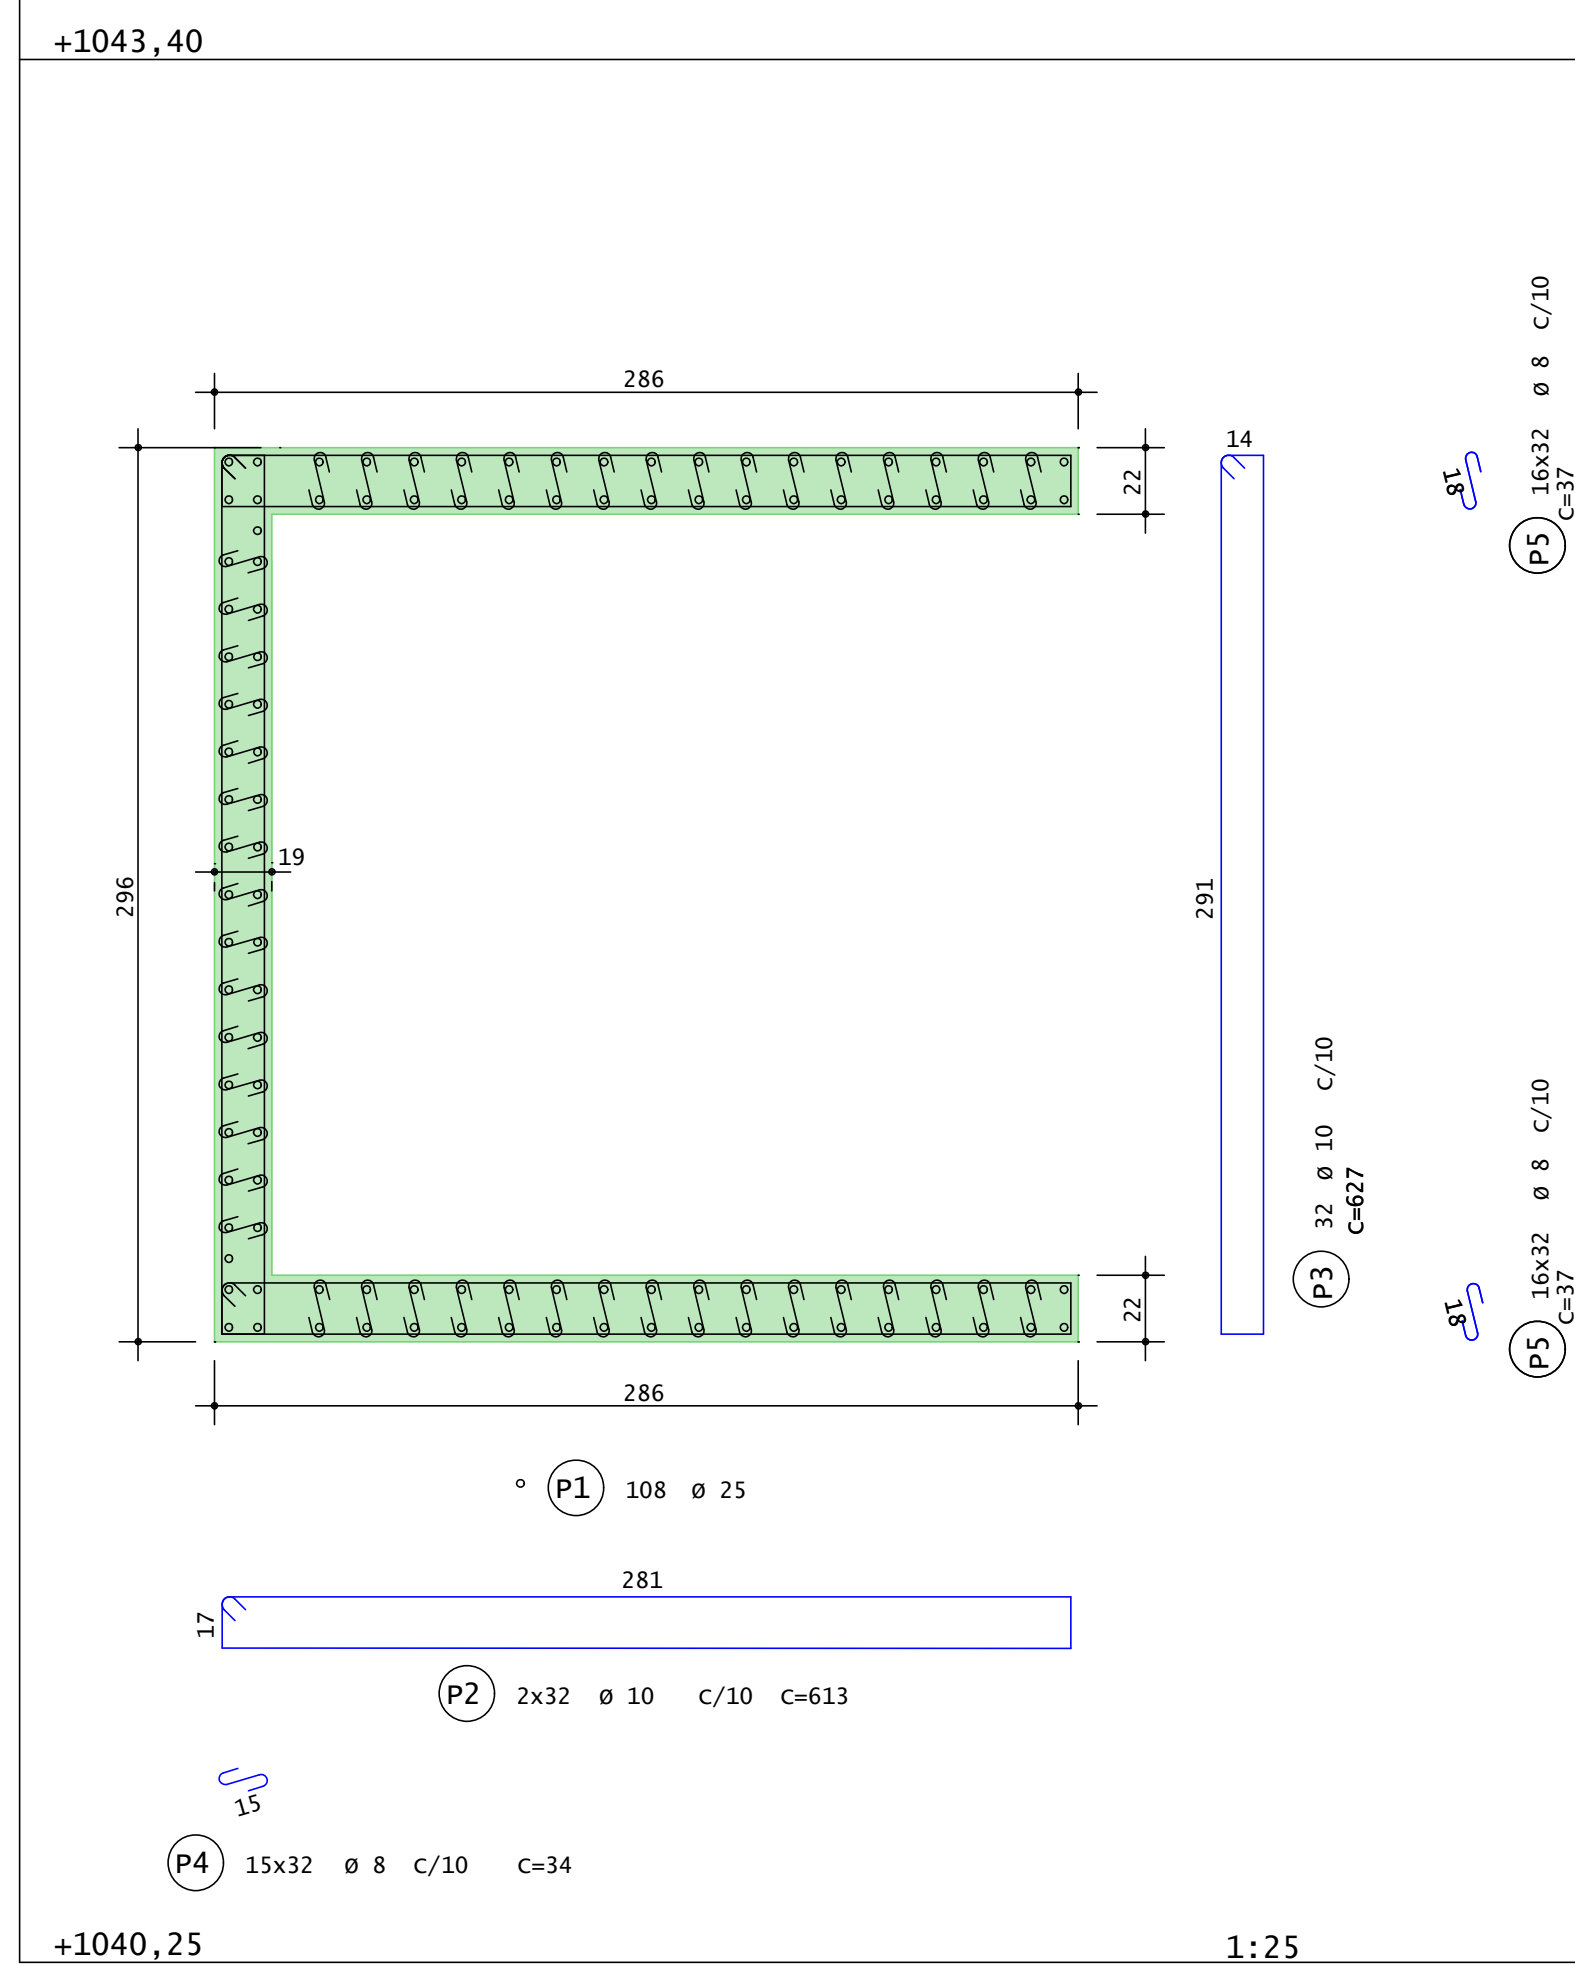
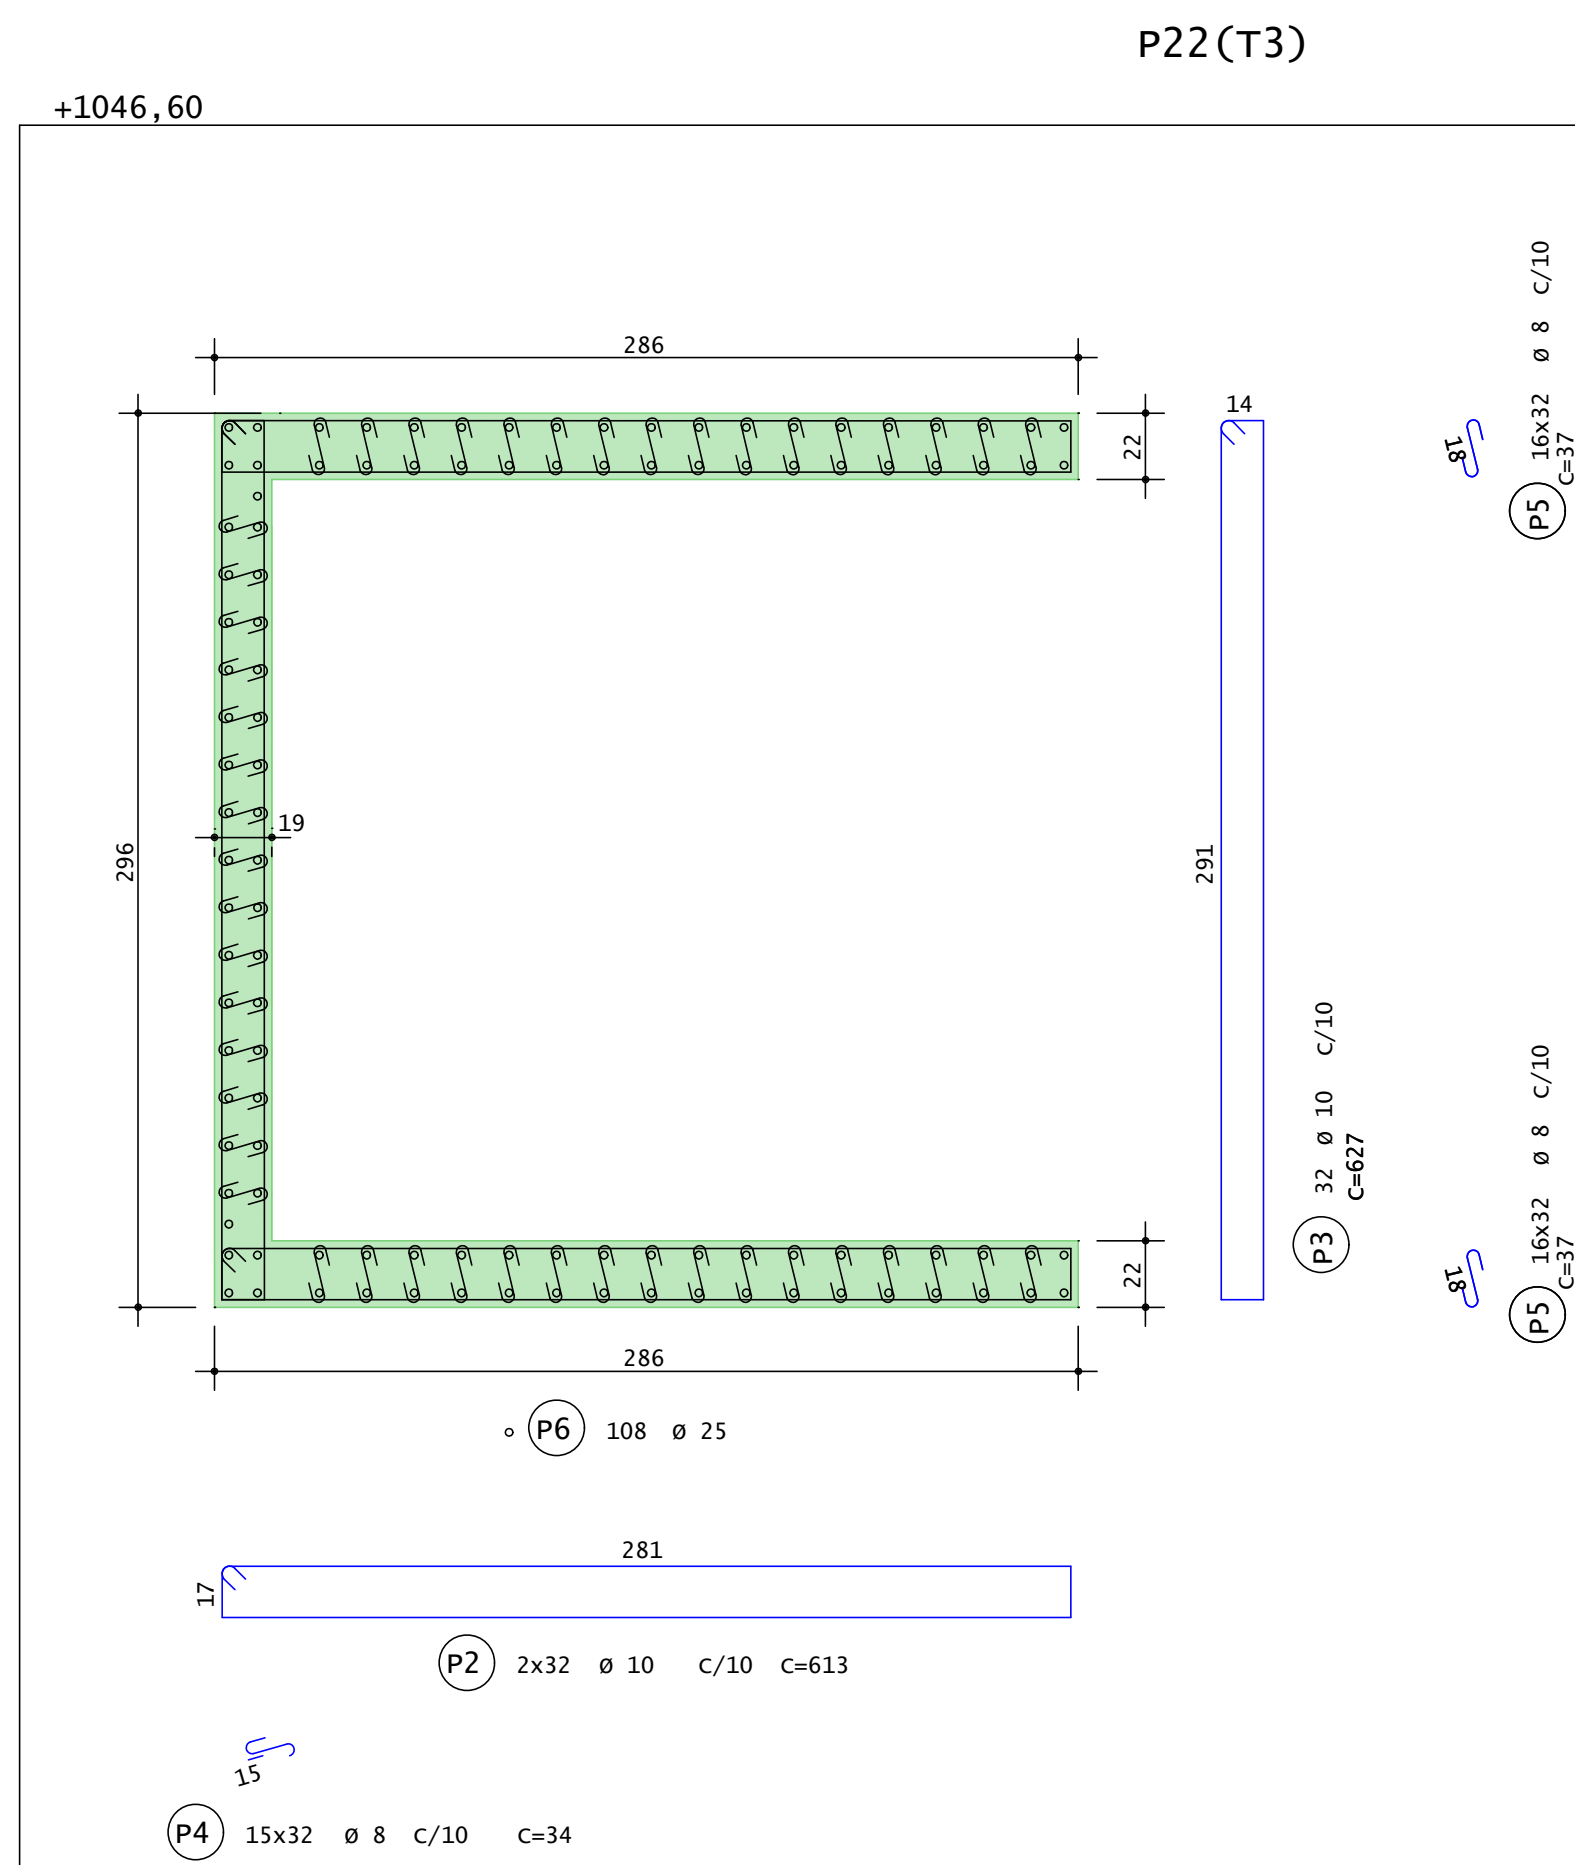
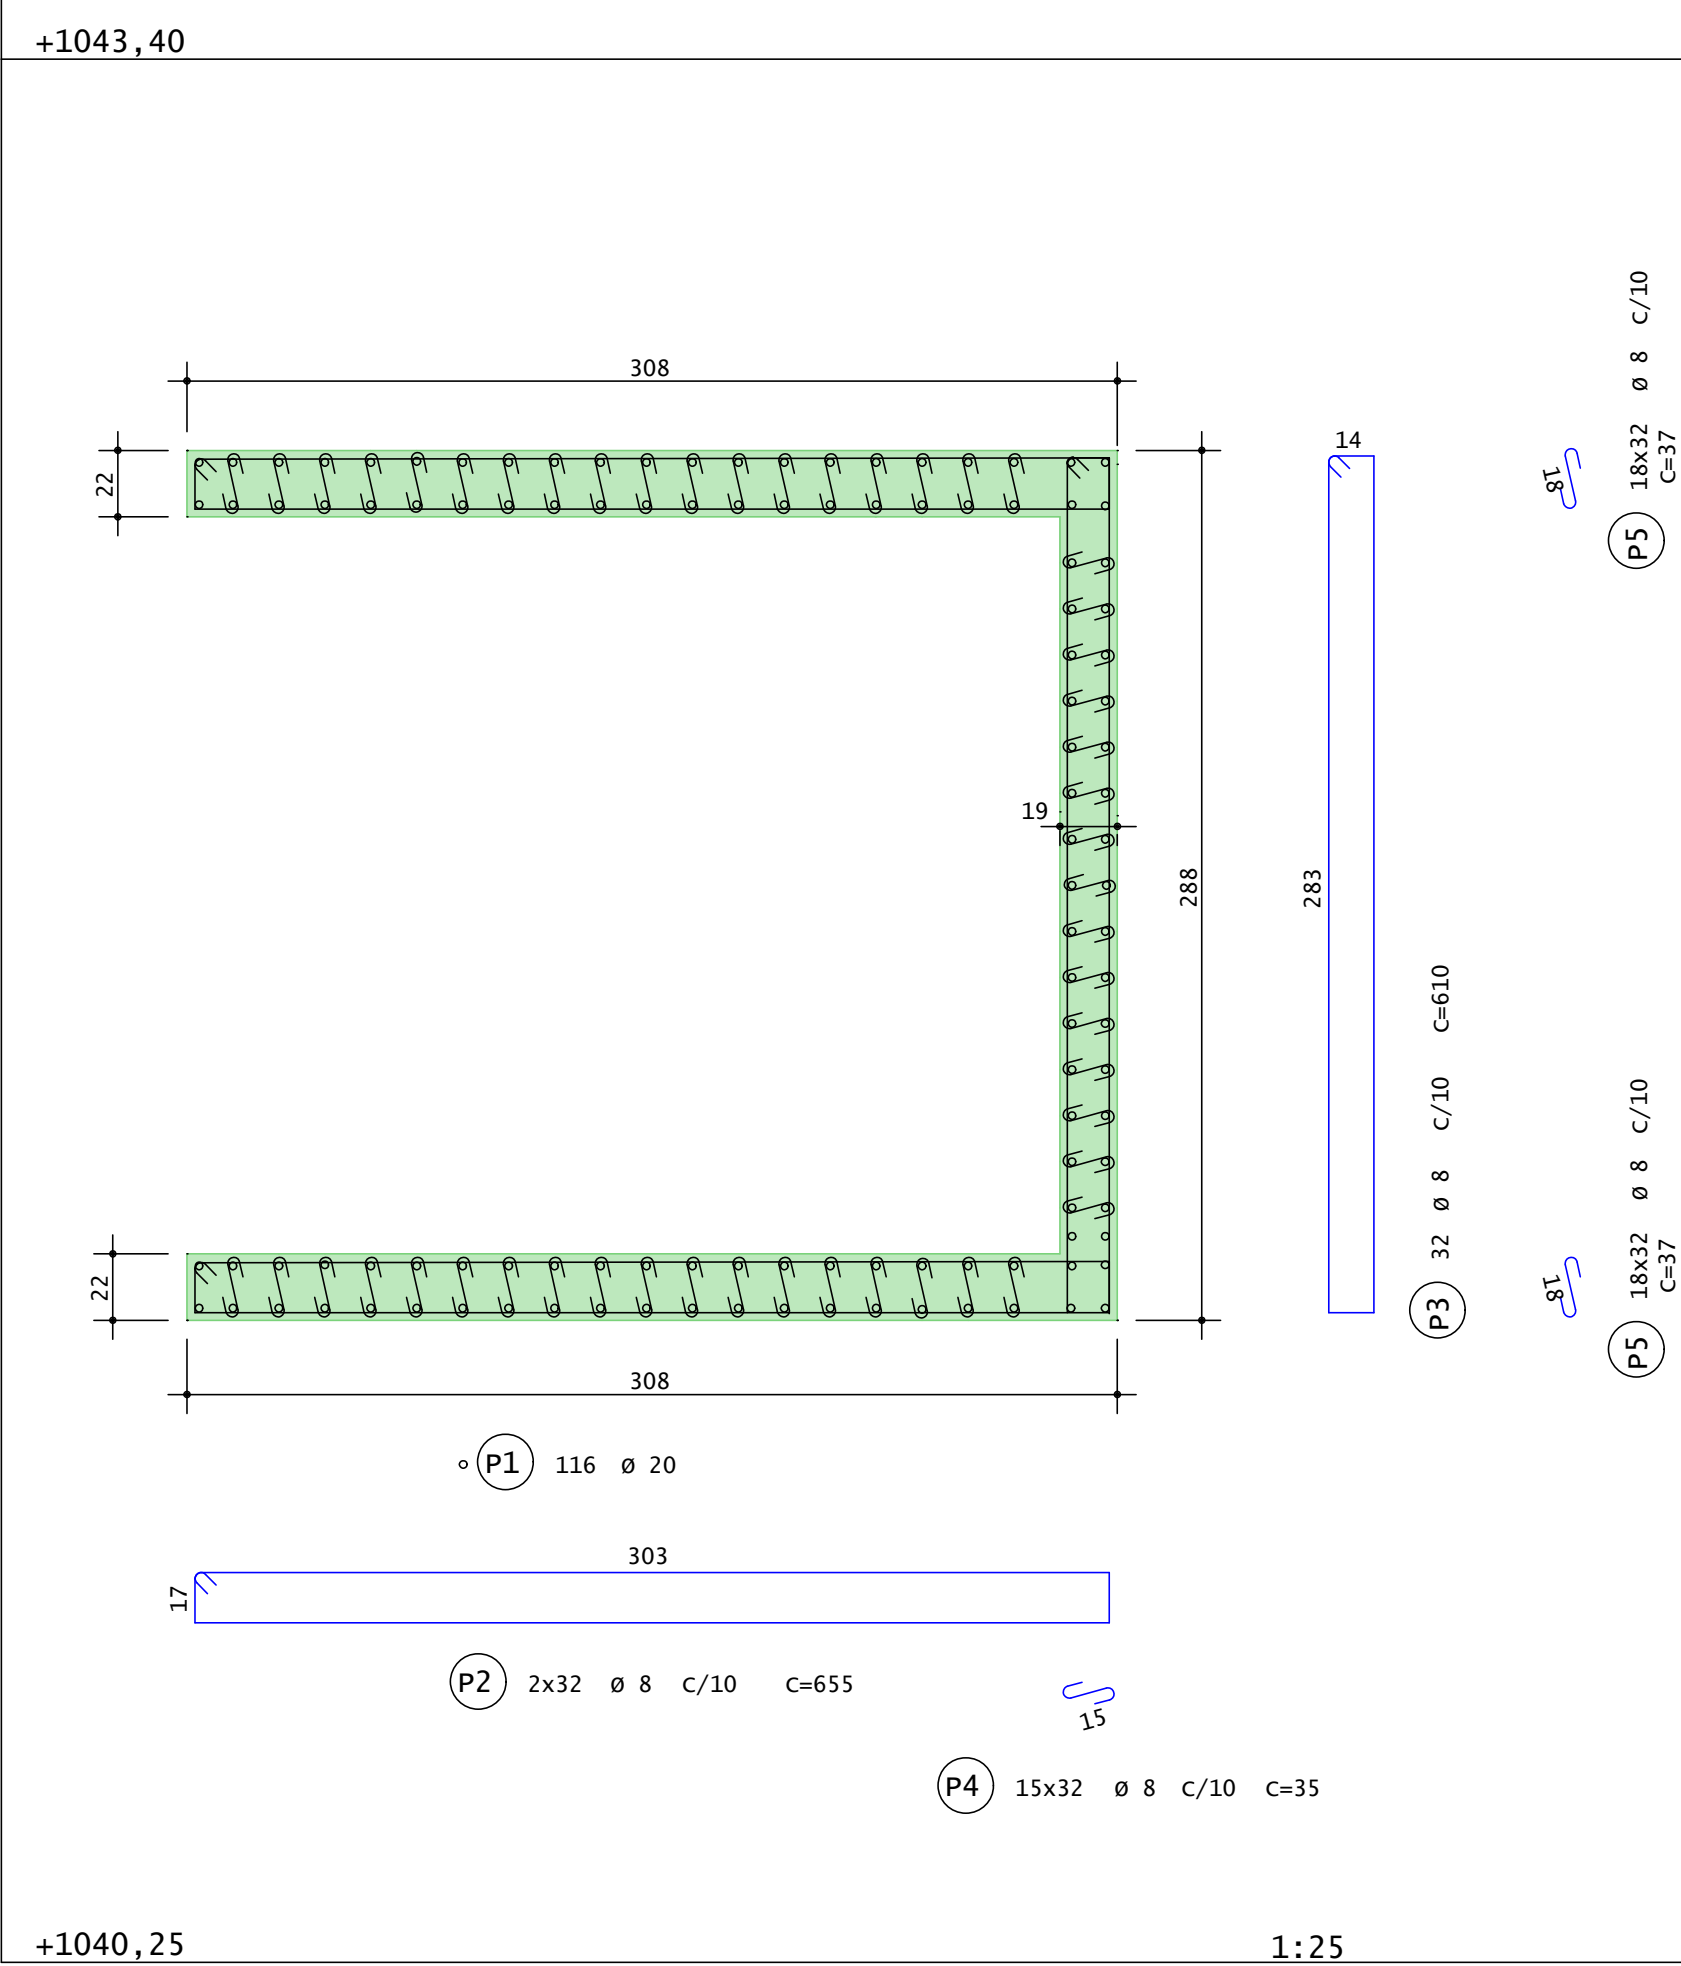


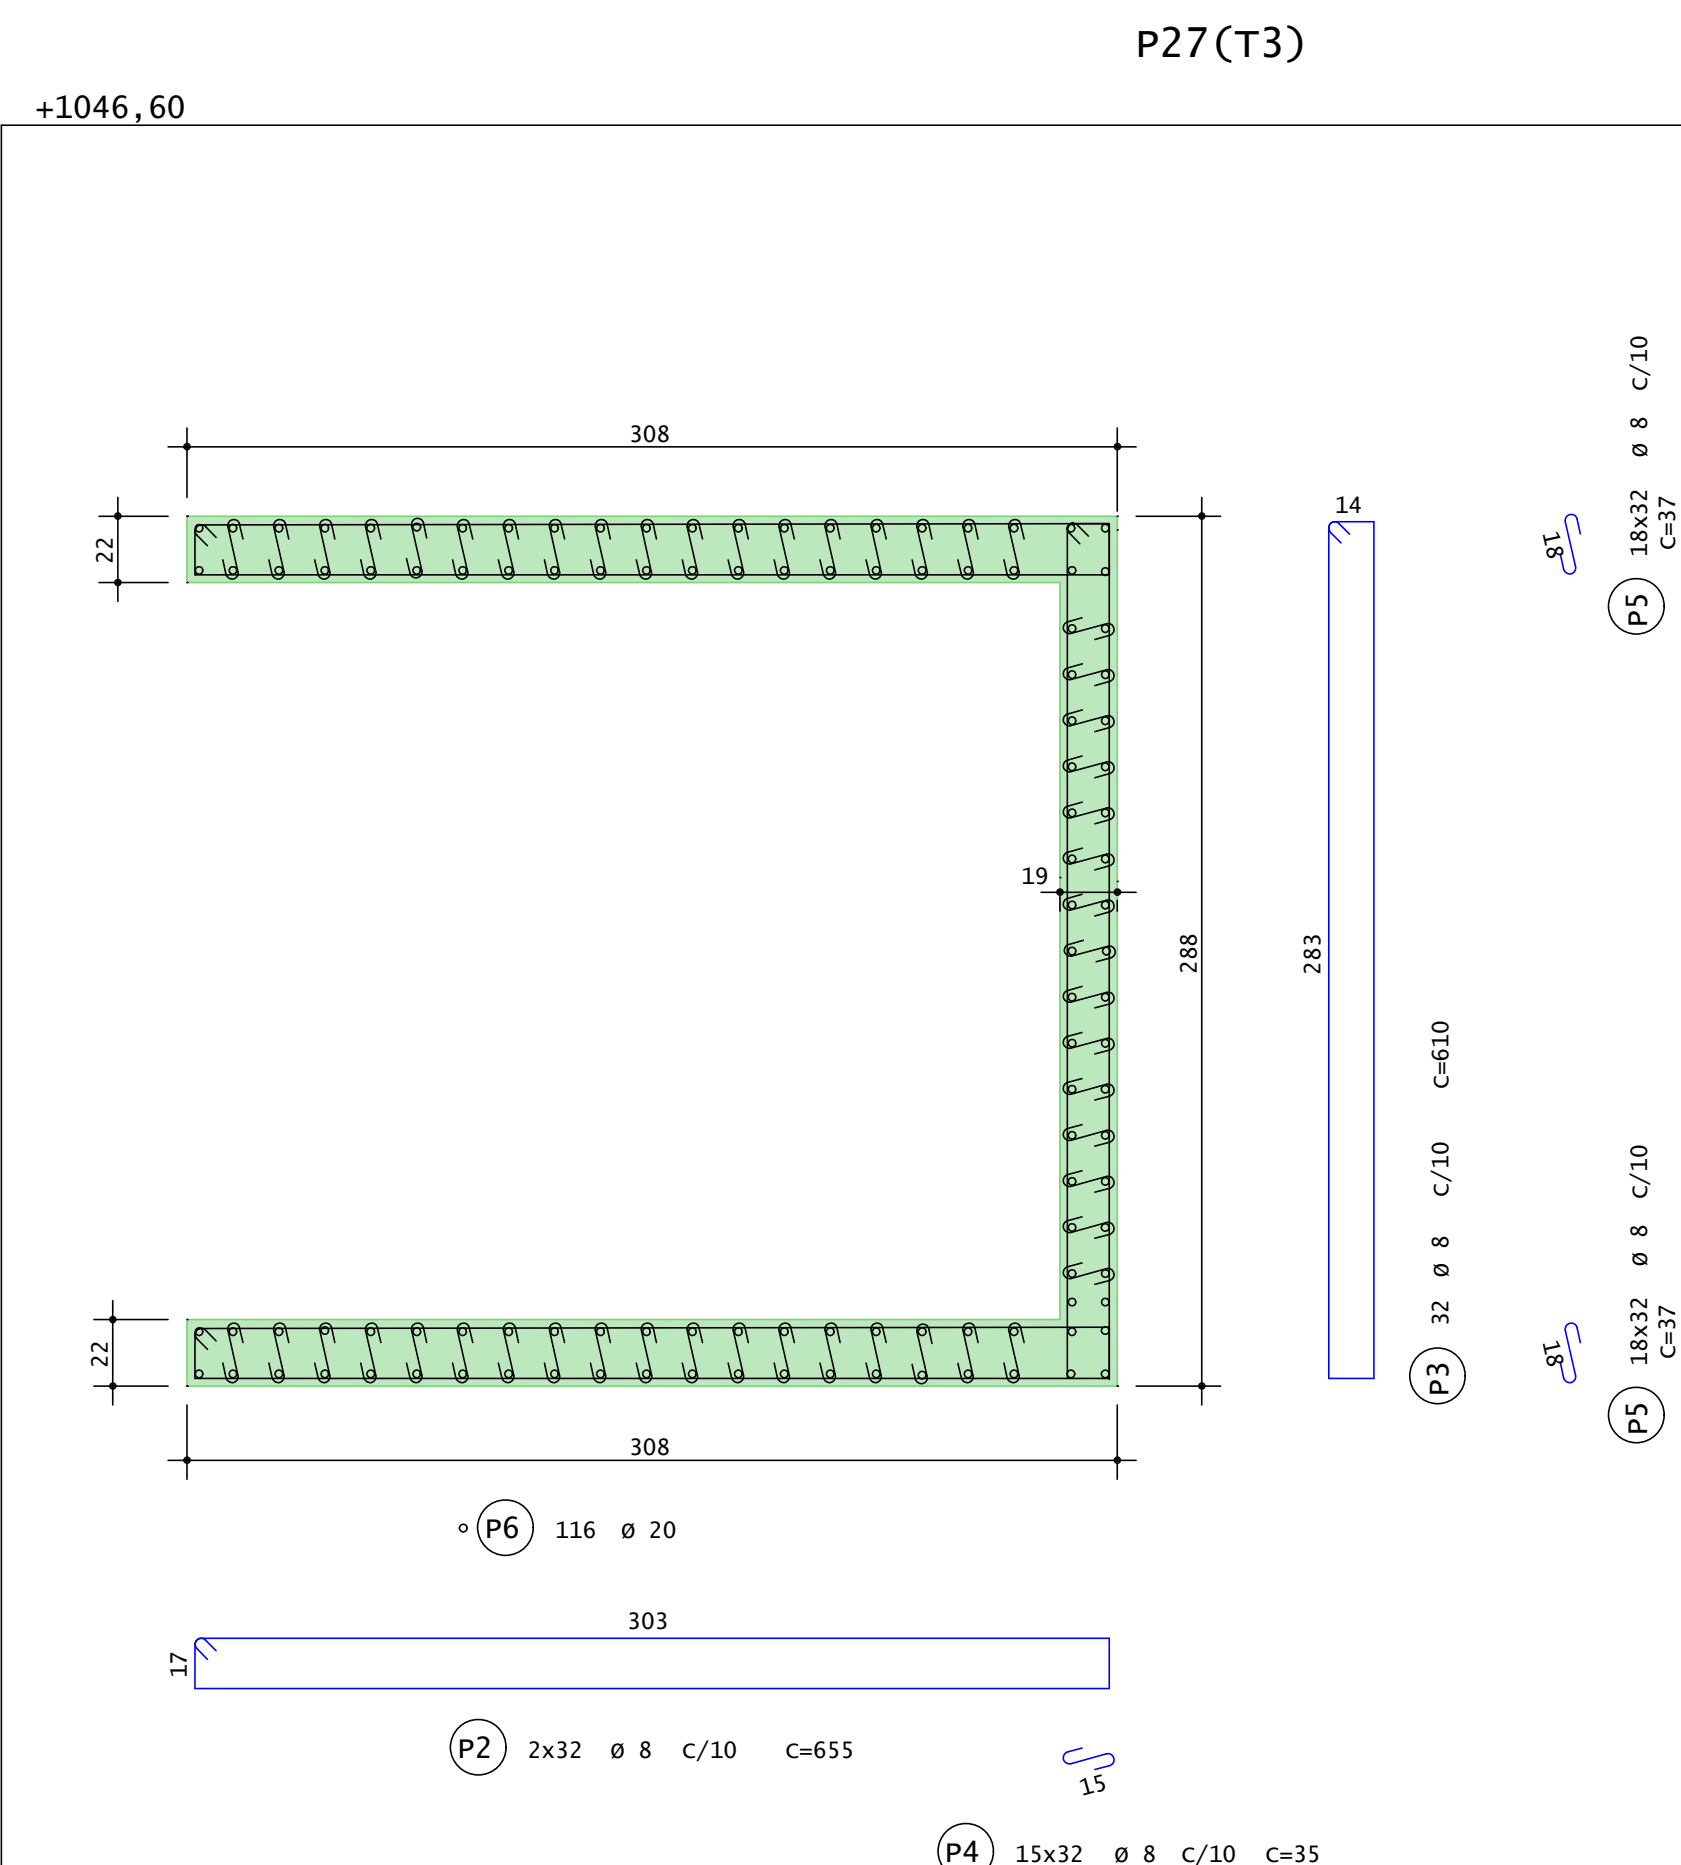

VER ESPERA NO DES. EPRO/SOMATTOS:
310-AURAT3-EST-EX-0127-ARMPIL-R00

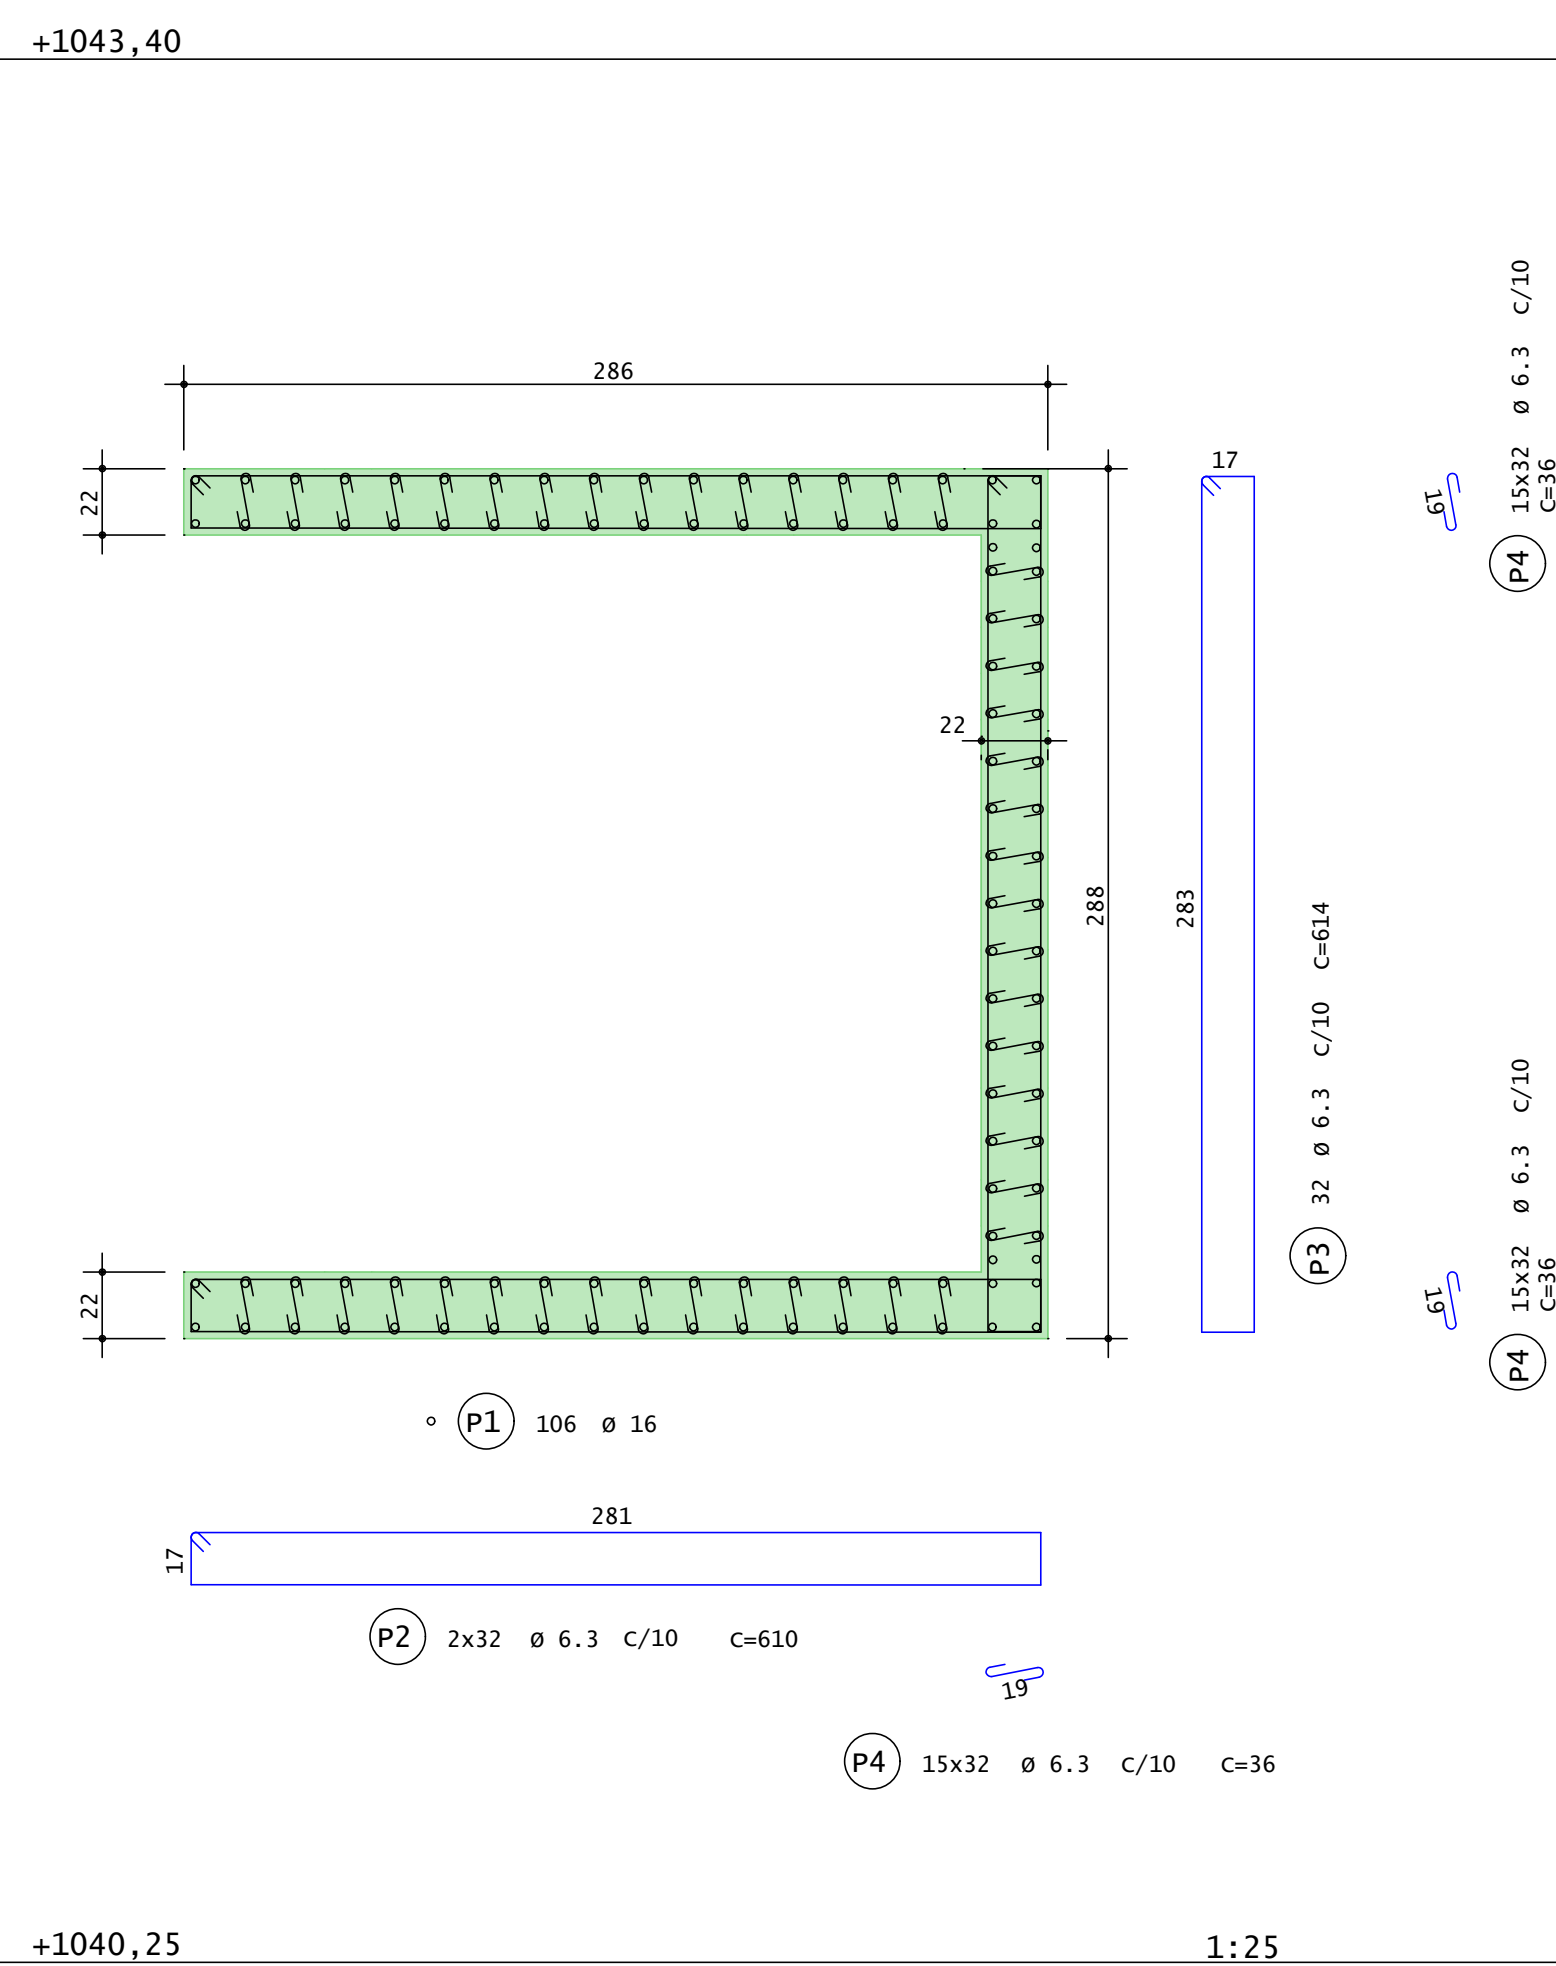

VER ESPERA NO DES. EPRO/SOMATTOS:
310-AURAT3-EST-EX-0127-ARMPIL-R00

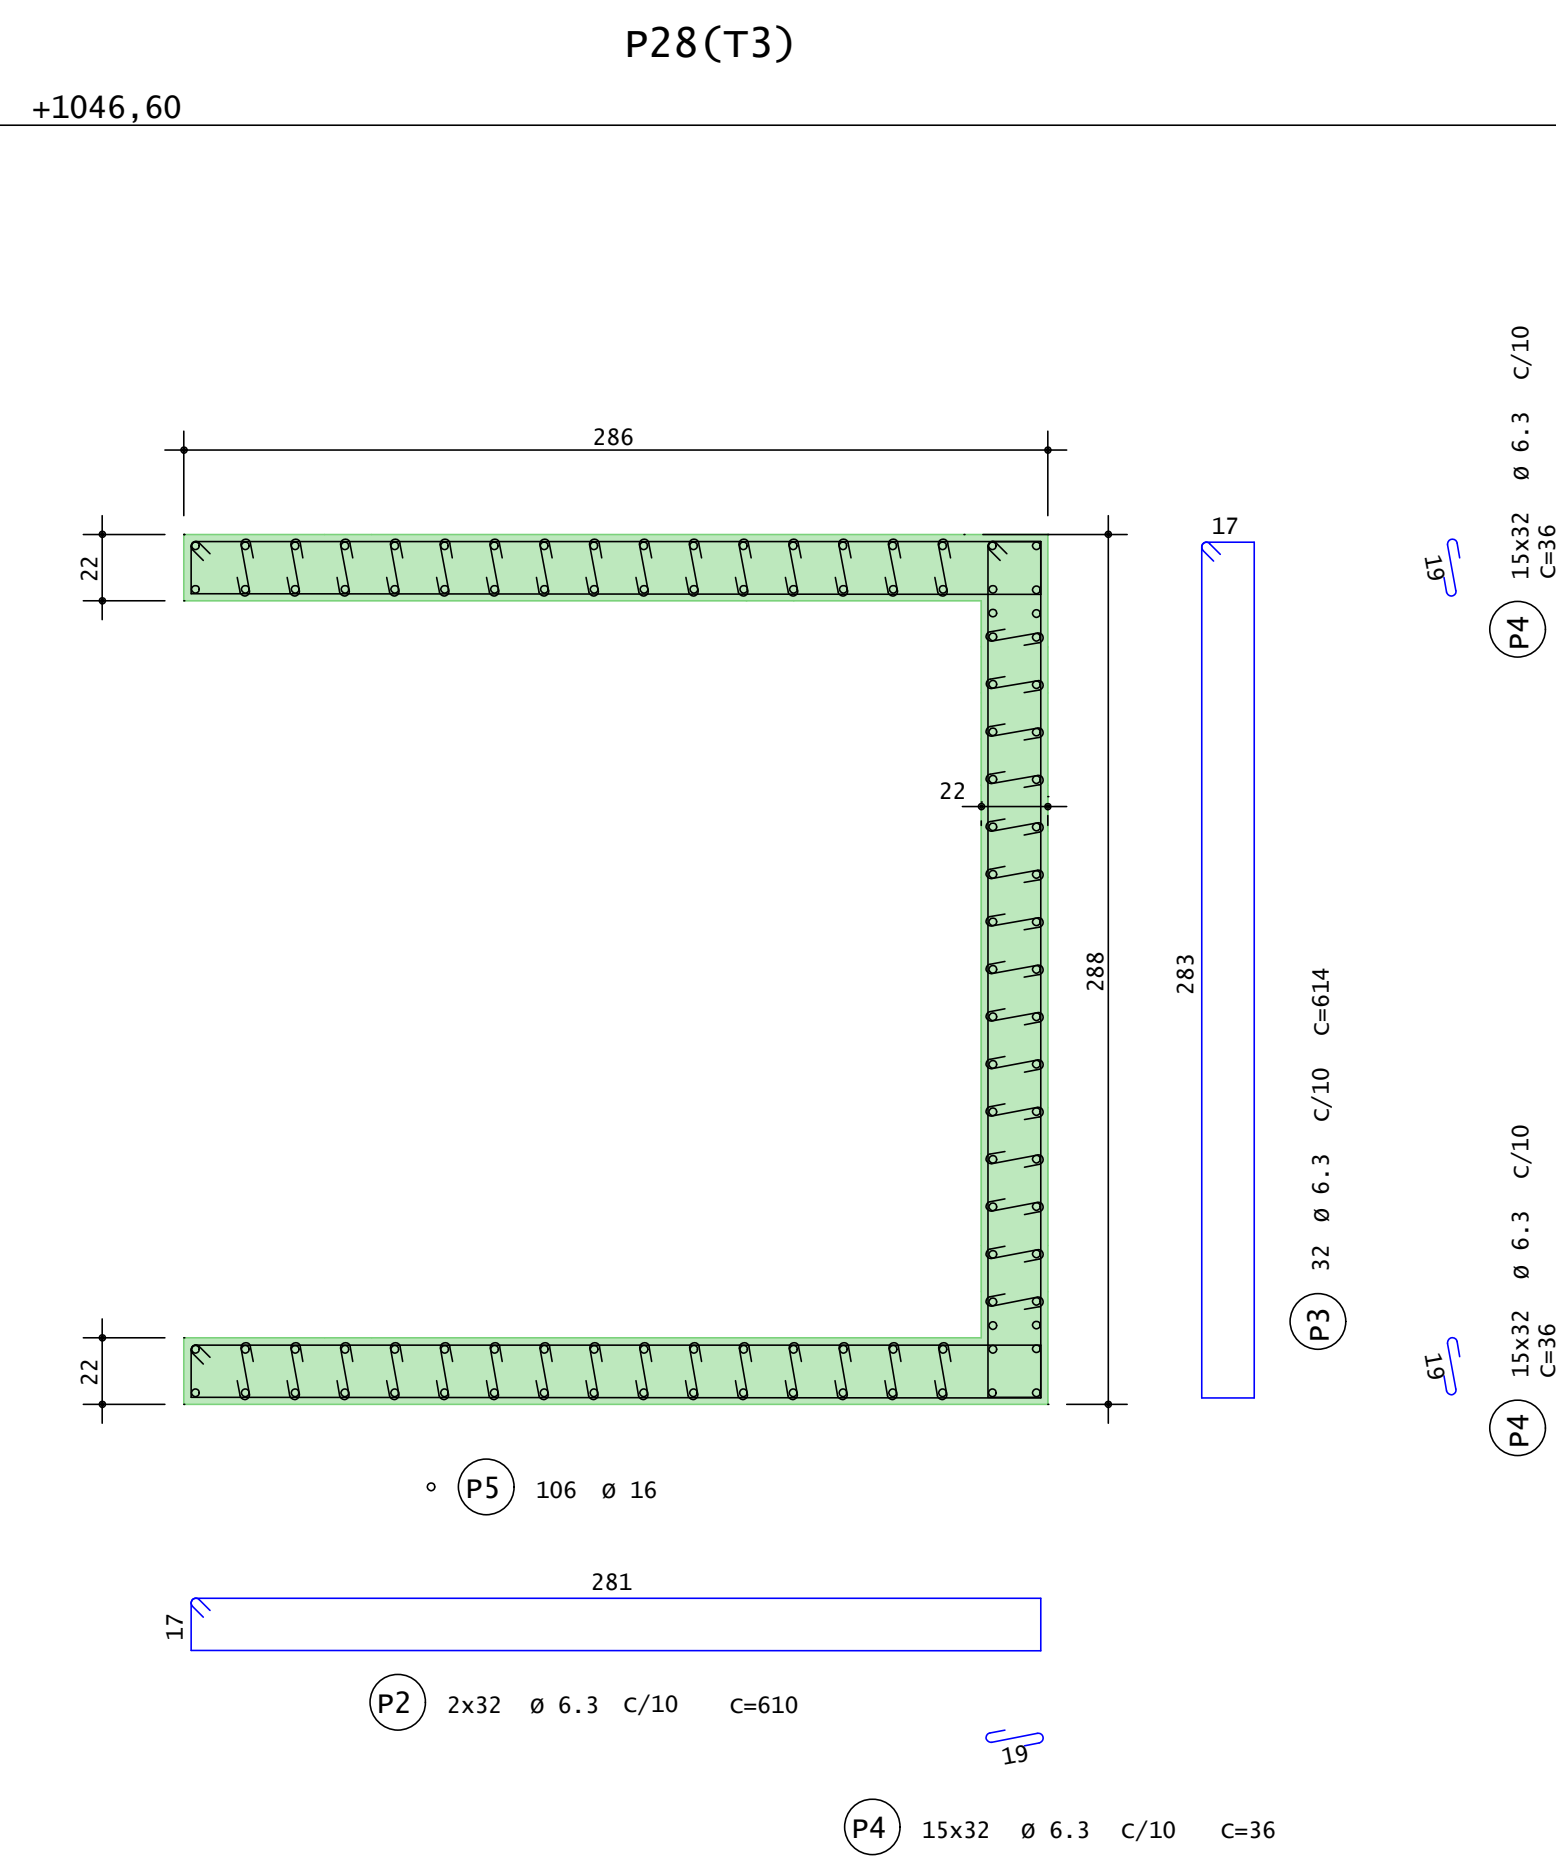

VER ESPERA NO DES. EPRO/SOMATTOS:
310-AURAT3-EST-EX-0127-ARMPIL-R00

	ACO	POS	BIT (mm)	QUANT	COMPLEMENT	
					(cm)	TOTAL (cm)
P22(T3)	50	1	25	108	385	41580
	50	2	10	128	613	78464
	50	4	10	102	617	80128
	50	4	8	960	34	32640
	50	5	8	2048	37	75776
	50	6	25	108	390	42120
P27(T3)	50	1	20	116	375	43920
	50	2	8	128	655	83840
	50	3	8	110	650	83040
	50	4	8	960	35	33600
	50	5	8	2304	38	47148
	50	6	20	116	385	42340
P28(T3)	50	1	16	106	360	38160
	50	2	6.3	128	610	76080
	50	3	6.3	64	614	39296
	50	4	6.3	2880	36	13680
	50	5	16	106	365	38690
	50	6	16	106	365	38690

RESUMO ACO CA 50-60				
ACO	BIT (mm)	COMPR (m)	PESO (kg)	
50	6,3	2211		542
50	8	3501		1385
50	10	1186		732
50	16	769		1213
50	20	853		2103
50	25	837		3225
Peso Total		50 =	9197 kgf	

PROJETOS COMPLEMENTARES EM REFERÊNCIA:

- 1- FORMA DO 3o. SUBSOLO - TORRE 3: DES. EPRO/SOMATTOS: 310-AURAEM-EST-EX-0027-3SUBS3-R02;
2- FORMA DO 2o. SUBSOLO - TORRE 3: DES. EPRO/SOMATTOS: 310-AURAEM-EST-EX-0029-2SUBS3-R02;
3- FORMA DO 1o. SUBSOLO - TORRE 3: DES. EPRO/SOMATTOS: 310-AURAEM-EST-EX-0031-1SUBS3-R02;

NORMAS ATENDIDAS

- 1- NBR 6118/2003: PROJETO DE ESTRUTURAS DE CONCRETO;
- 2- NBR 14931/2004: EXECUÇÃO DE ESTRUTURAS DE CONCRETO - PROCEDIMENTO;
- 3- NBR 5674/2004: MANUTENÇÃO DE EDIFICAÇÕES-REQUISITOS PARA O SISTEMA DE GESTÃO E MANUTENÇÃO;
- 4- NBR 6120/2003: AÇÕES PARA CÁLCULO DE ESTRUTURA DE EDIFICAÇÕES;
- 5- NBR 6122/2019/Enl:2022: PROJETO E EXECUÇÃO DE FUNDAÇÕES;
- 6- NBR 15575/2024: EDIFICAÇÕES HABITACIONAIS - PREVENÇÃO E REPARAÇÃO DE UMIDADE;
- 7- NBR 6123/2003: FORÇAS DEVIDAS AO VENTO EM EDIFICAÇÕES;
- 8- NBR 15200/2024: PROJETO DE ESTRUTURAS DE CONCRETO EM SITUAÇÃO DE INCÊNDIO;
- 9- NBR 17170/2022: EDIFICAÇÕES - GARANTIAS - PRAZOS RECOMENDADOS E DIRETRIZES;

NOTAS GERAIS:

- 1- COTAS EM CENTÍMETRO, NÍVEIS EM METRO;
2- CONCRETO ESTRUTURAL:
- FCK $\geq$ 40,0 MPa;
- FATOR ÁGUA/CEMENTO (A/C) $\leq$ 0,60
- CONSUMO MÍNIMO DE CIMENTO = 280 kg/m³;
- TEMPO DE CURA CONFORME CONDIÇÕES CLIMÁTICAS, MÍNIMO DE 7 (SETE) DIAS;
3- MÓDULO DE ELASTICIDADE INICIAL DO CONCRETO NR 618/2023:
 $E_{ci} = 5600 \sqrt{f_{ck}}$ (DADOS EM MPa) - $\alpha_{CE}=1,0$ PARA GRANITO E GNAISSE:
PARA FCK $\geq$ 40,0 MPa - $E_{ci} = 33130$ MPa;
4- COBRIMENTO = 2,5 cm;
5- AÇOS CA 50;

05			
04			
03			
02			
01			
00	EMISSÃO INICIAL	Rosana	22/09/25
N°	HISTÓRICO REVISÕES	RESPONSÁVEL	DATA

PROPRIETÁRIO:	
---------------	--

	SOMATTOS PATRIMIR Q4 40 EMPREEND.IMOBILIÁRIOS SPE LTDA CNPJ : 42.306.807/0001-05
	AUTOR DO PROJETO: TOSSEI MIRANDA ARQUITETURA E CONSULTORIA LTDA CREA : 8447-6
	RESPONSÁVEL TÉCNICO EXECUÇÃO: BERNARDO IMPELLIZZIERI SÁ MATTOIS CREA : 82679/D MG
	RESPONSÁVEL TÉCNICO PROJ., EXECUTIVO: EPRO ENGENHARIA DE PROJETOS E CONSULTORIA S/C LTDA CREA : 6154/MG
ENGENHEIRO COLABORADOR: LUIZ RENATO DE LIMA CREA : 26927/D	

EMPREENDIMENTO:

CÓDIGO: 310 - AURA - TORRE 3

LOGAL :	DATA :
---------	--------

LOCAL: RUA CEI GABRIEL FELIPE FARIA VILA DA SERRA - NOVA LIMA - MG

NOVA CEET GABRIEL FLEURY FARIAS; FIAZ DA SILVA	NOVA ESPRIMO	RG	JARDIMATIVES

PROJETO: DATA 1a. EMISSÃO: 22/09/2025

PROJETO EXECUTIVO	22/09/2025
-------------------	------------

ESTRUTURAL	REVISÃO: 500	
------------	-----------------	--

	R00

CONTEÚDO:	
ARMACÃO DOS PILARES DO NÍVEL +1040,25 a +1046,60	ESCALA:

3o. SUBSOLO AO 1o. SUBSOLO (3a. PARTE)	INDICADA
--	----------