
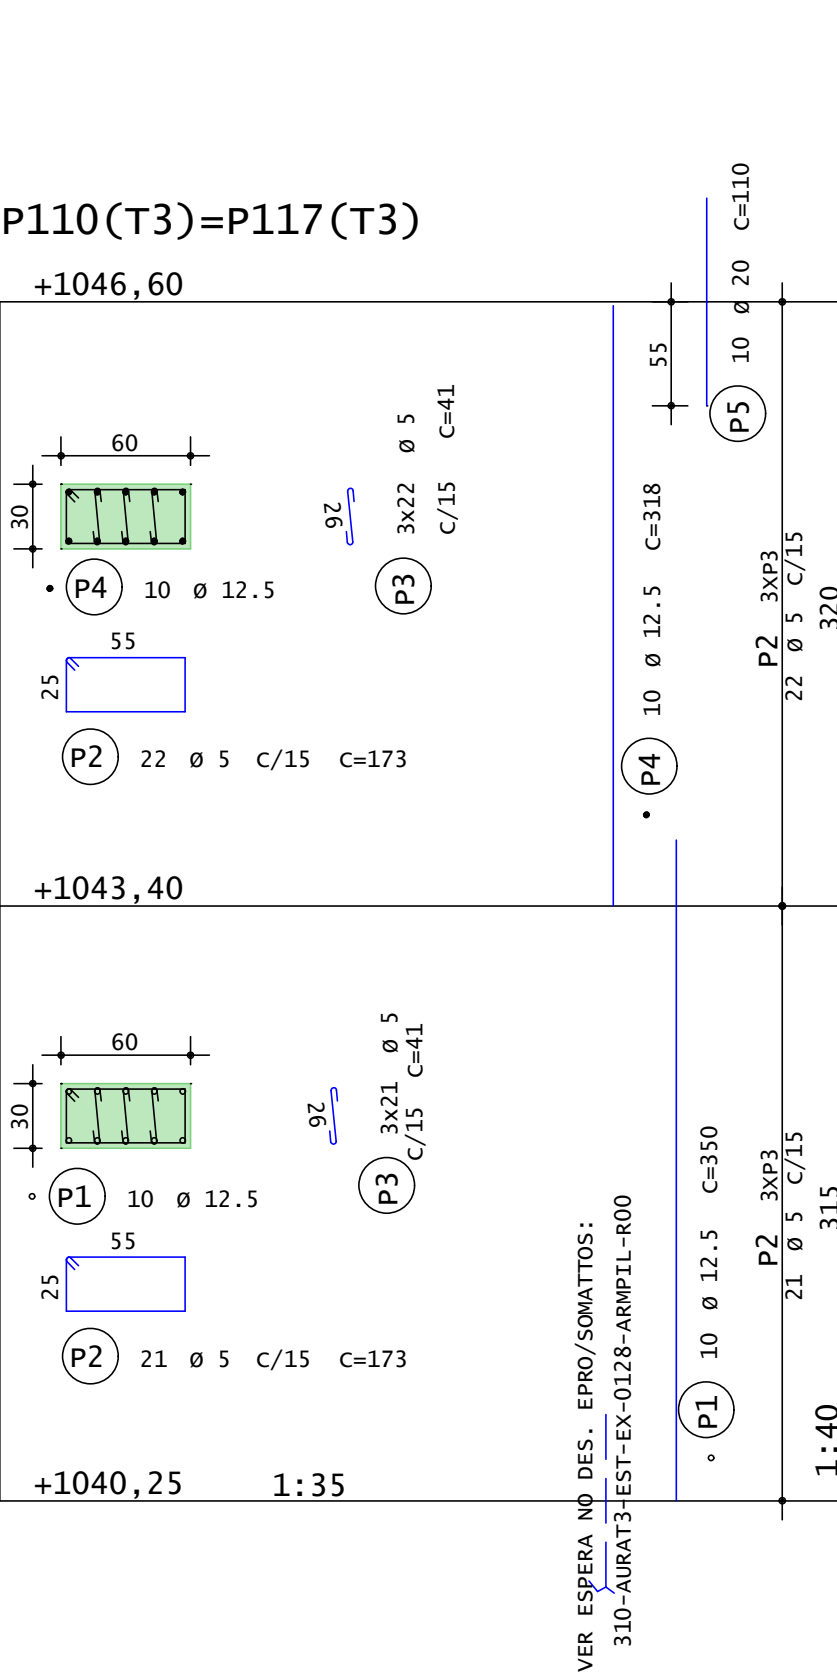
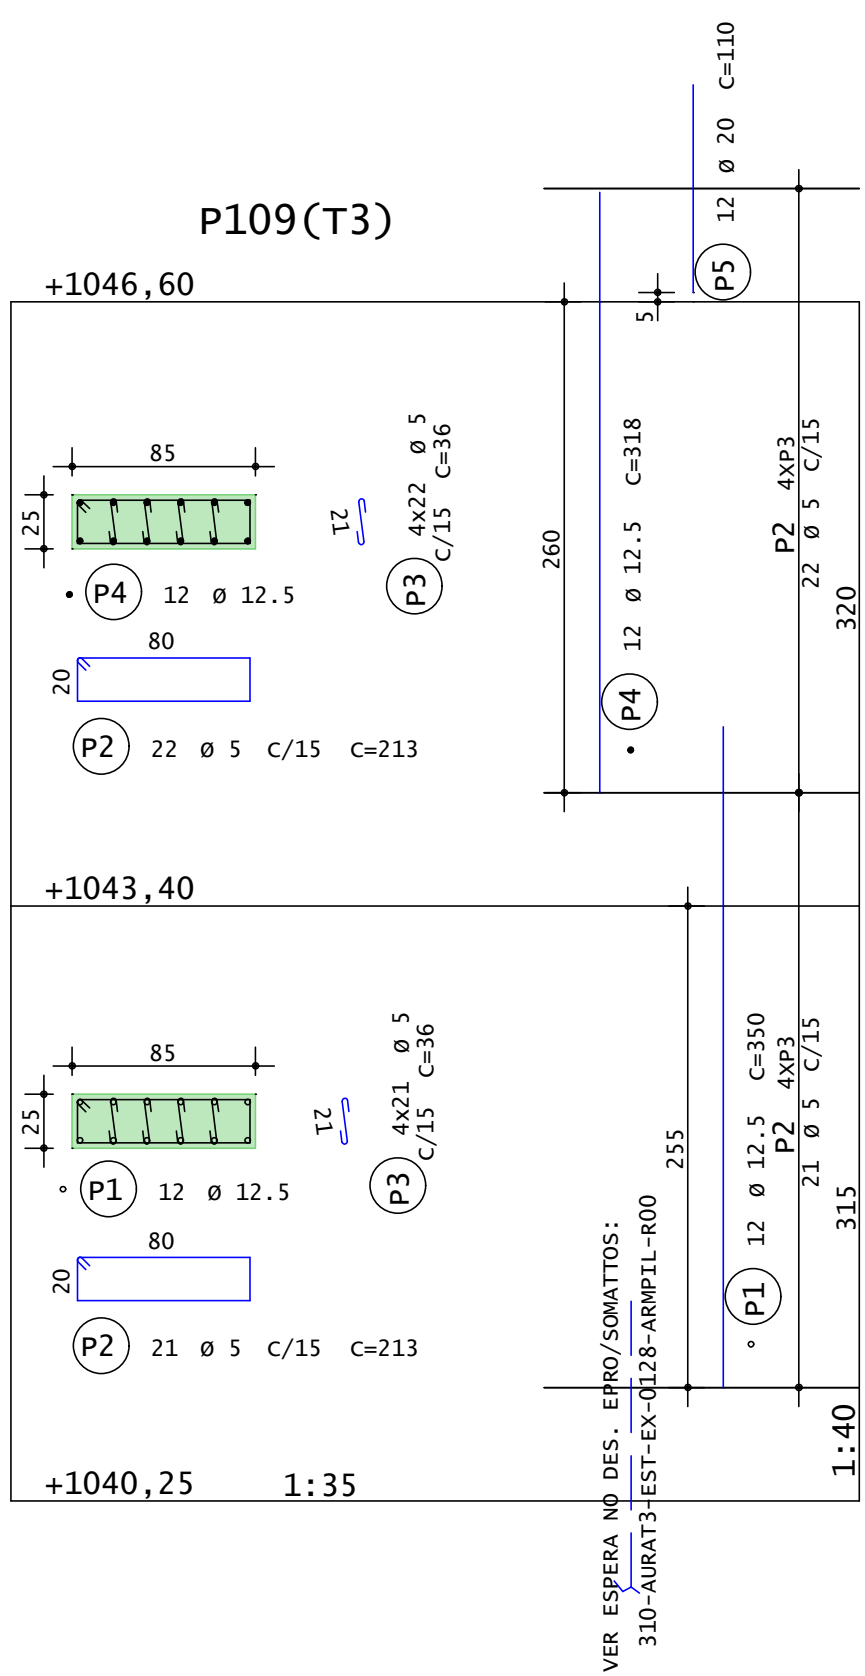
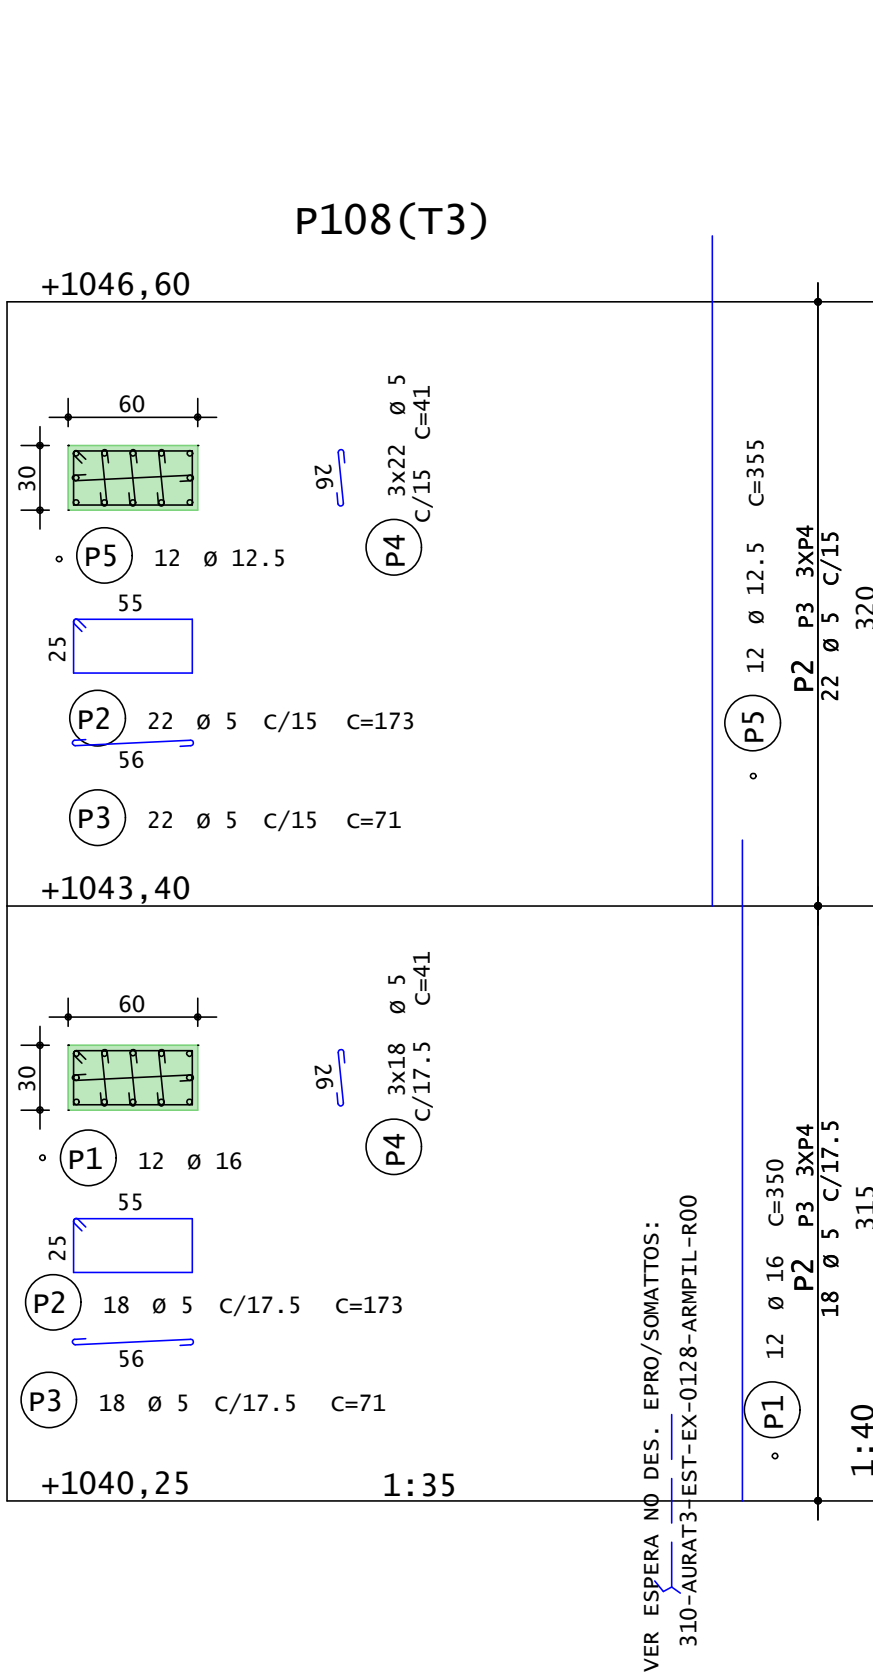
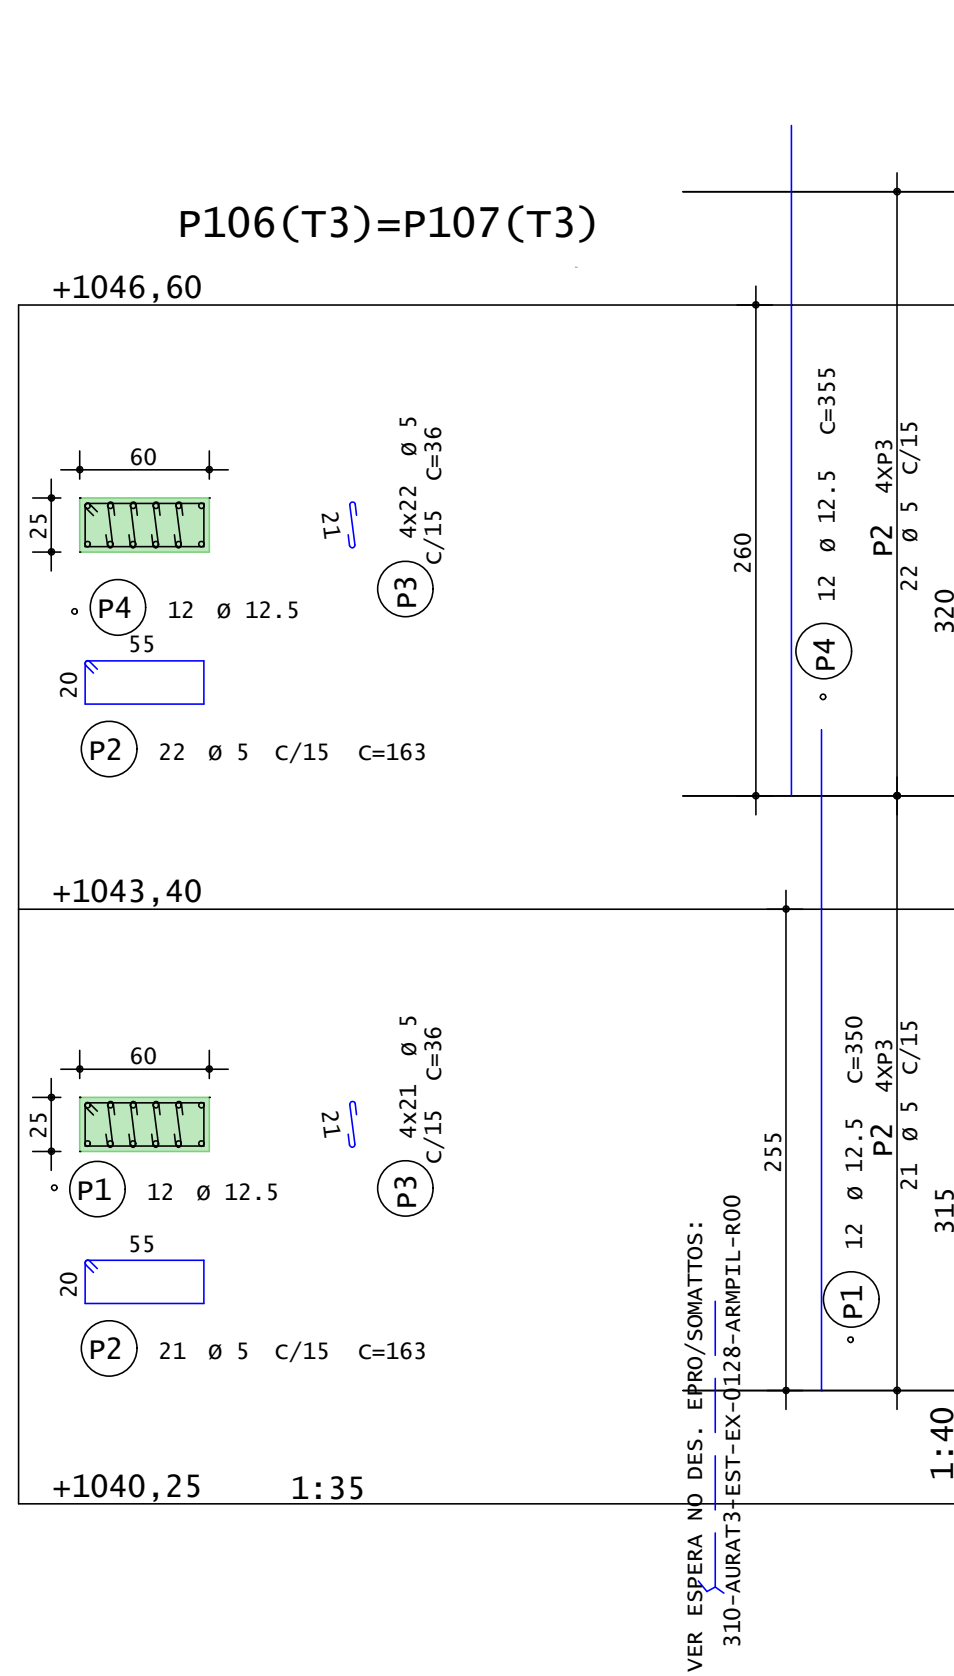
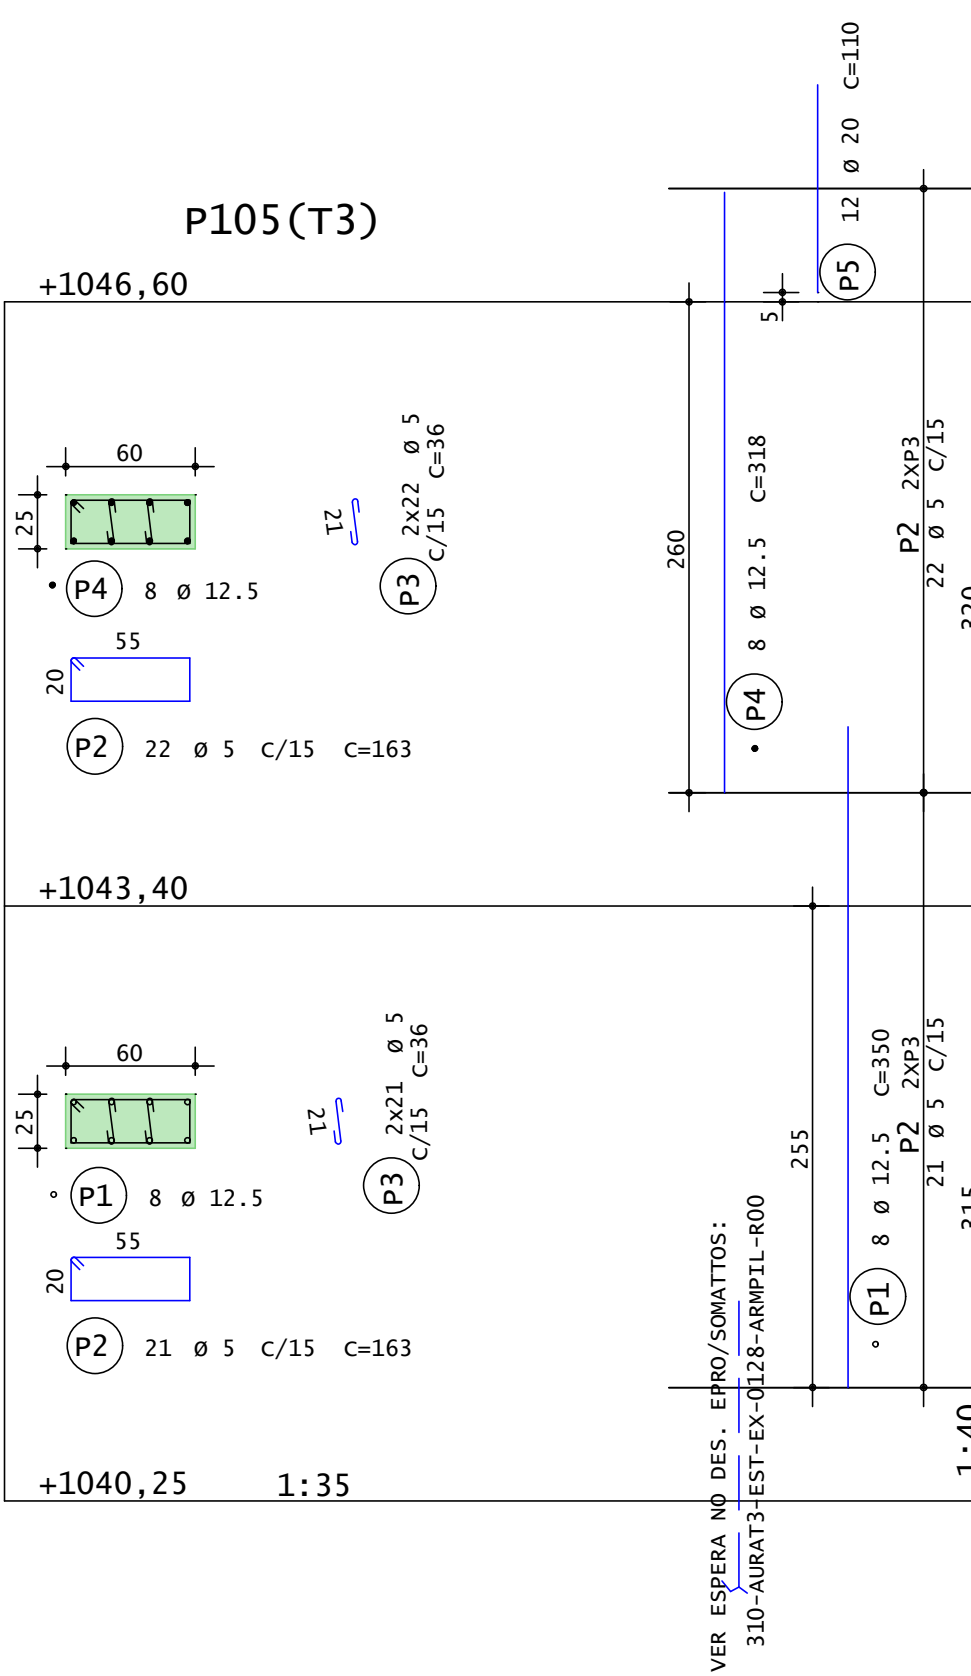
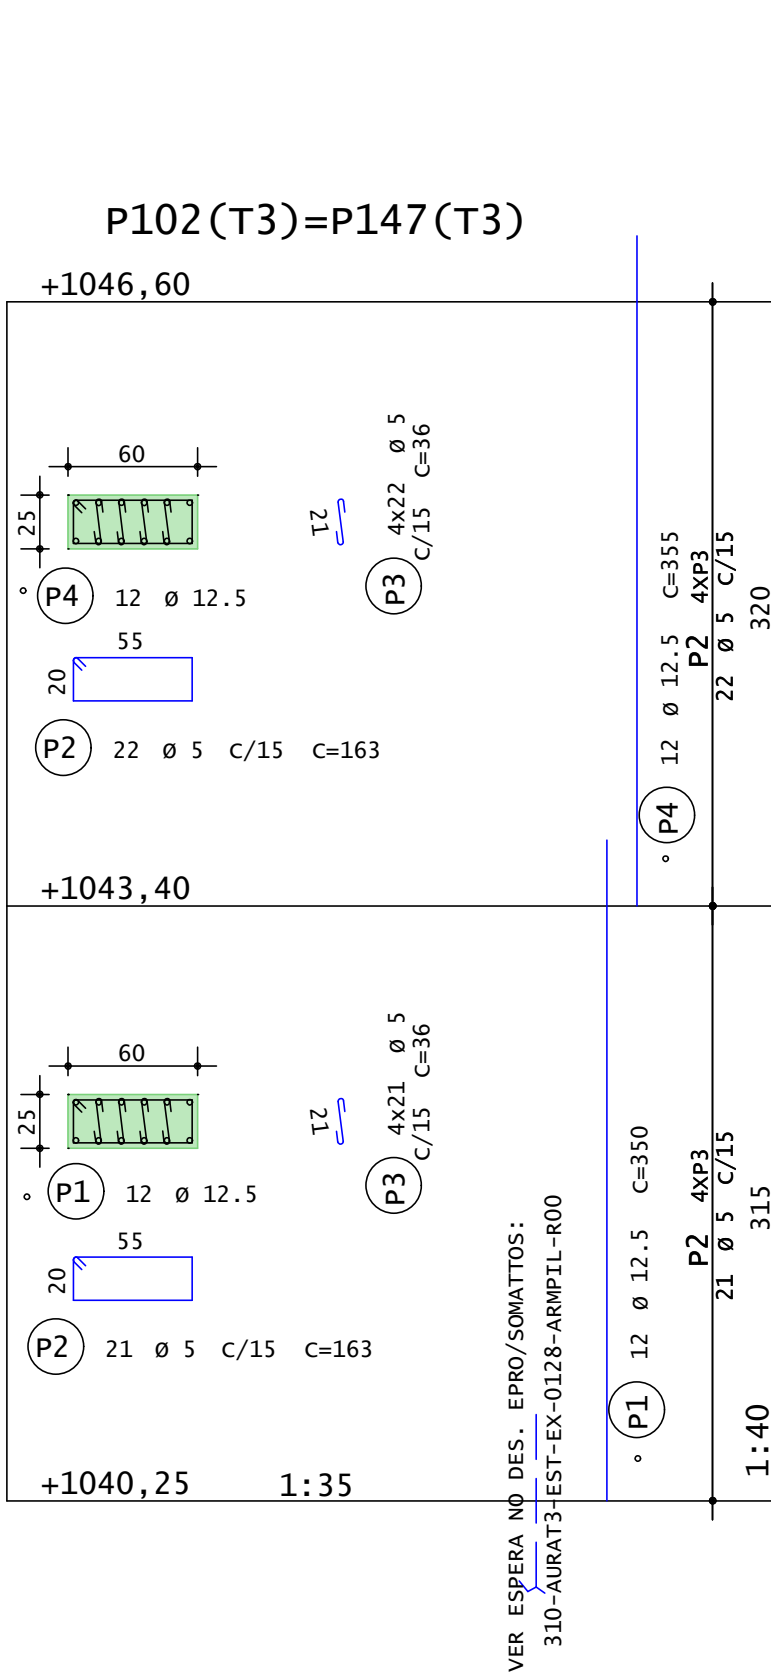
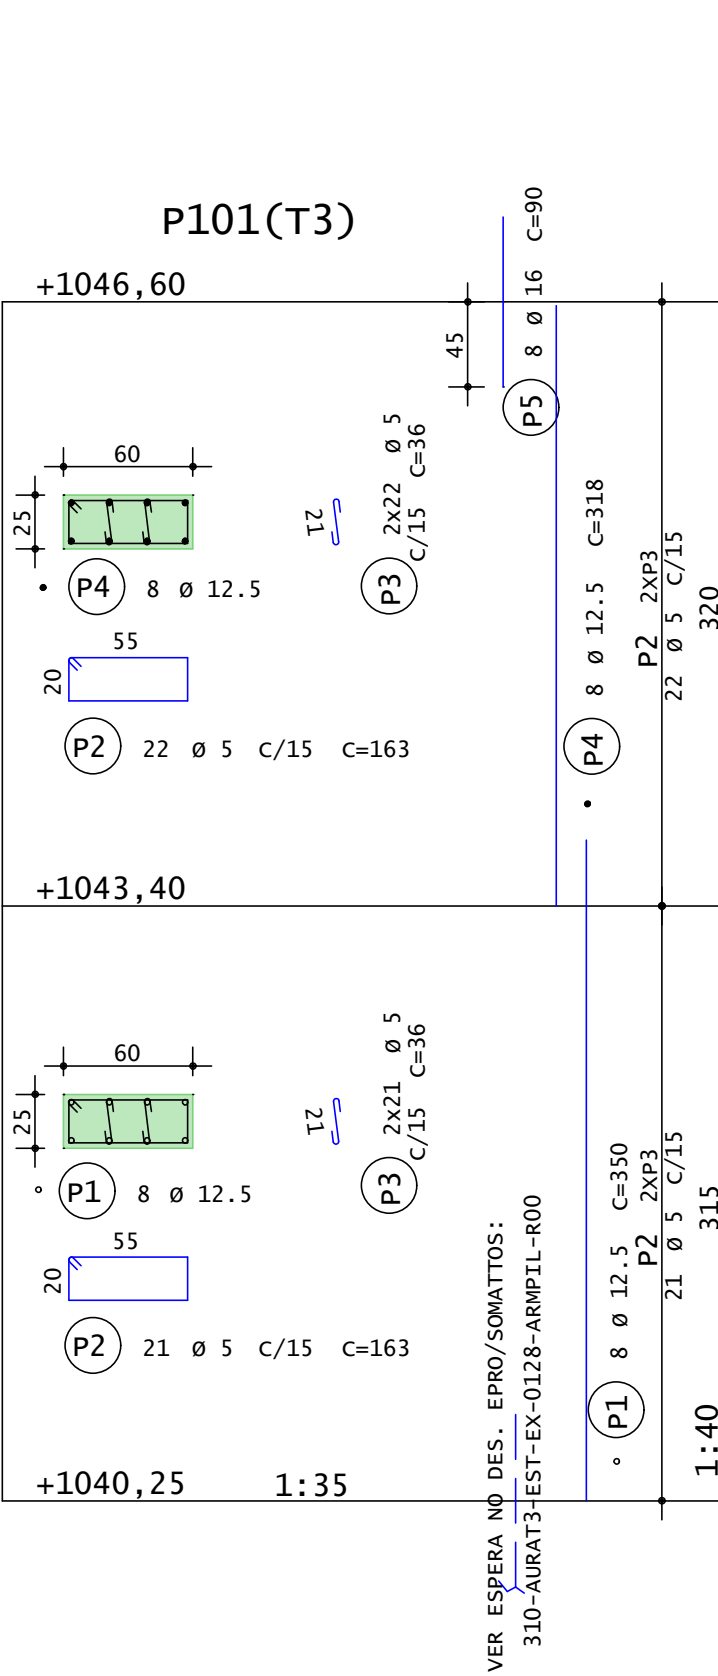
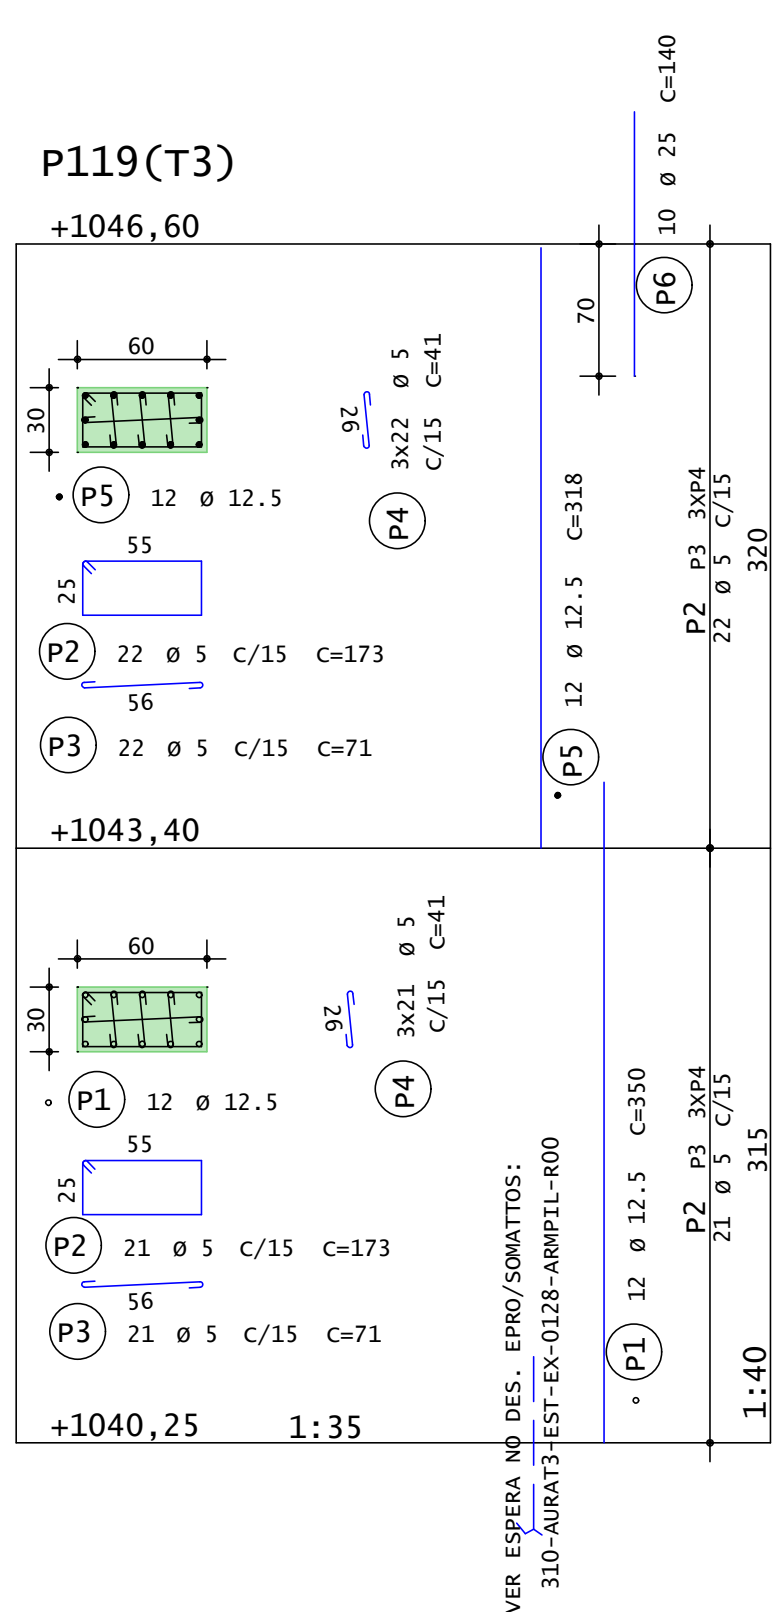
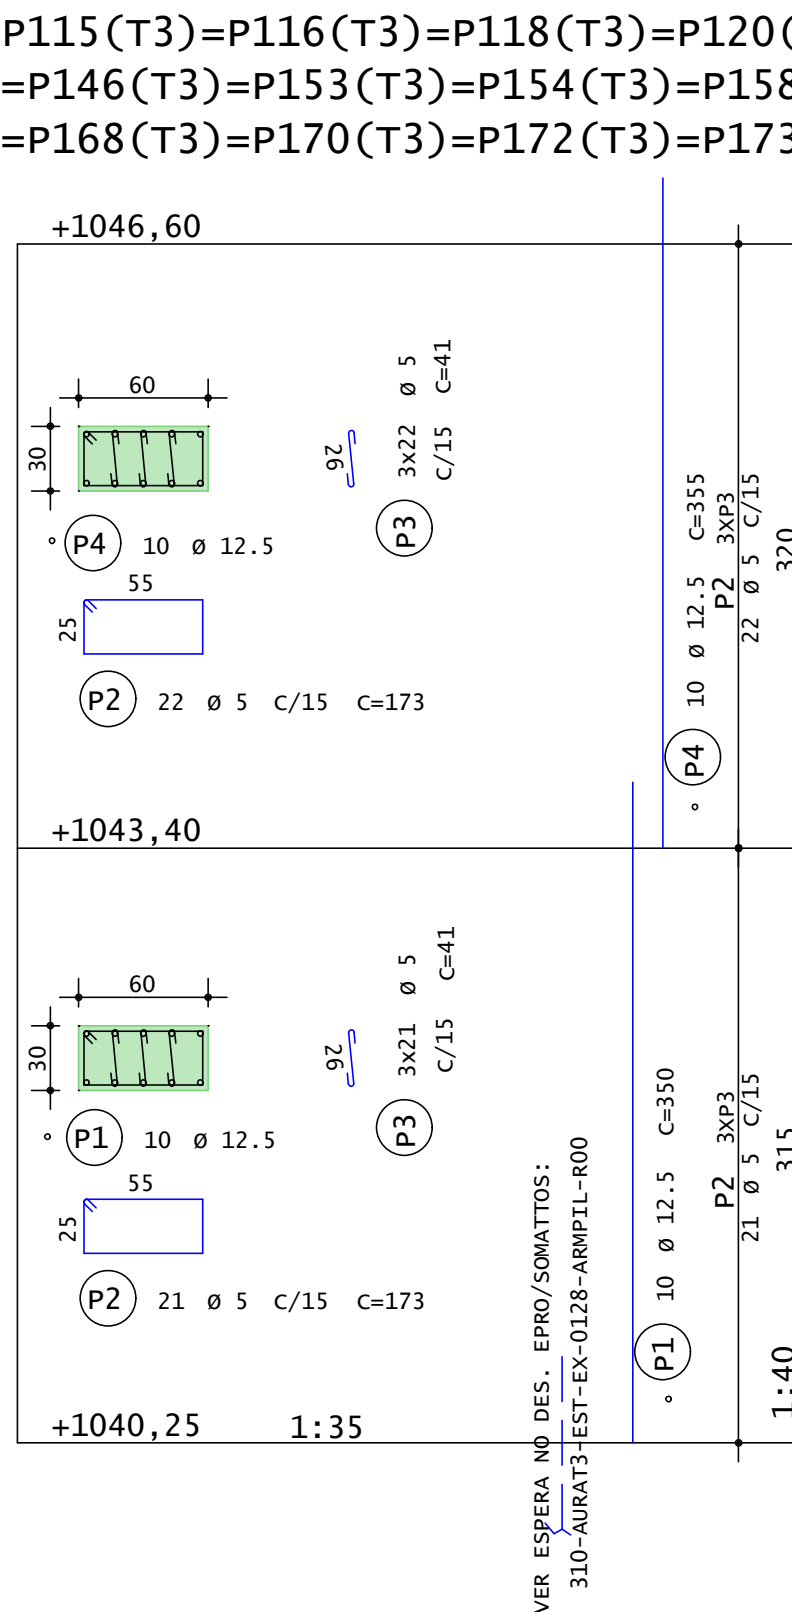
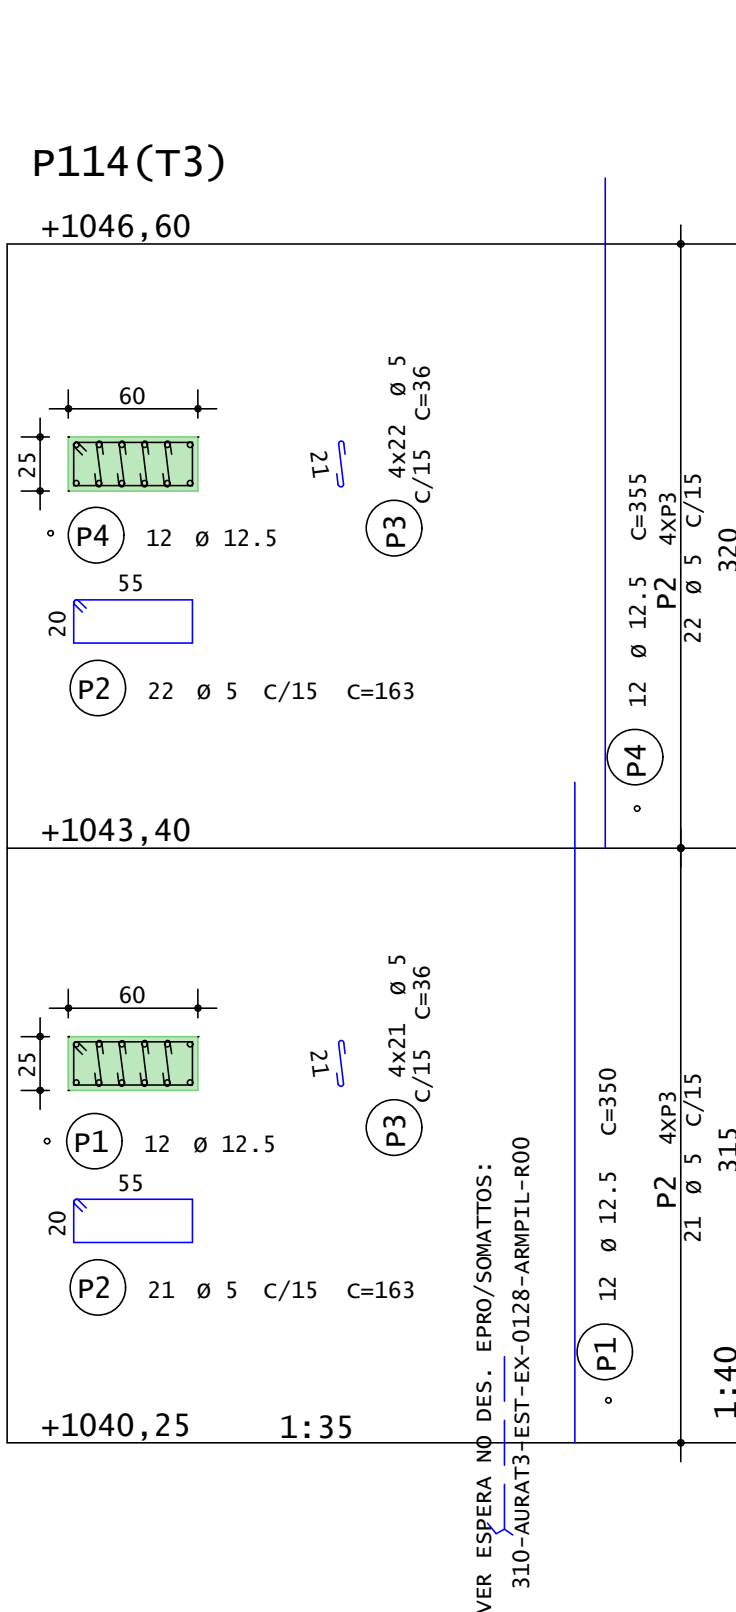
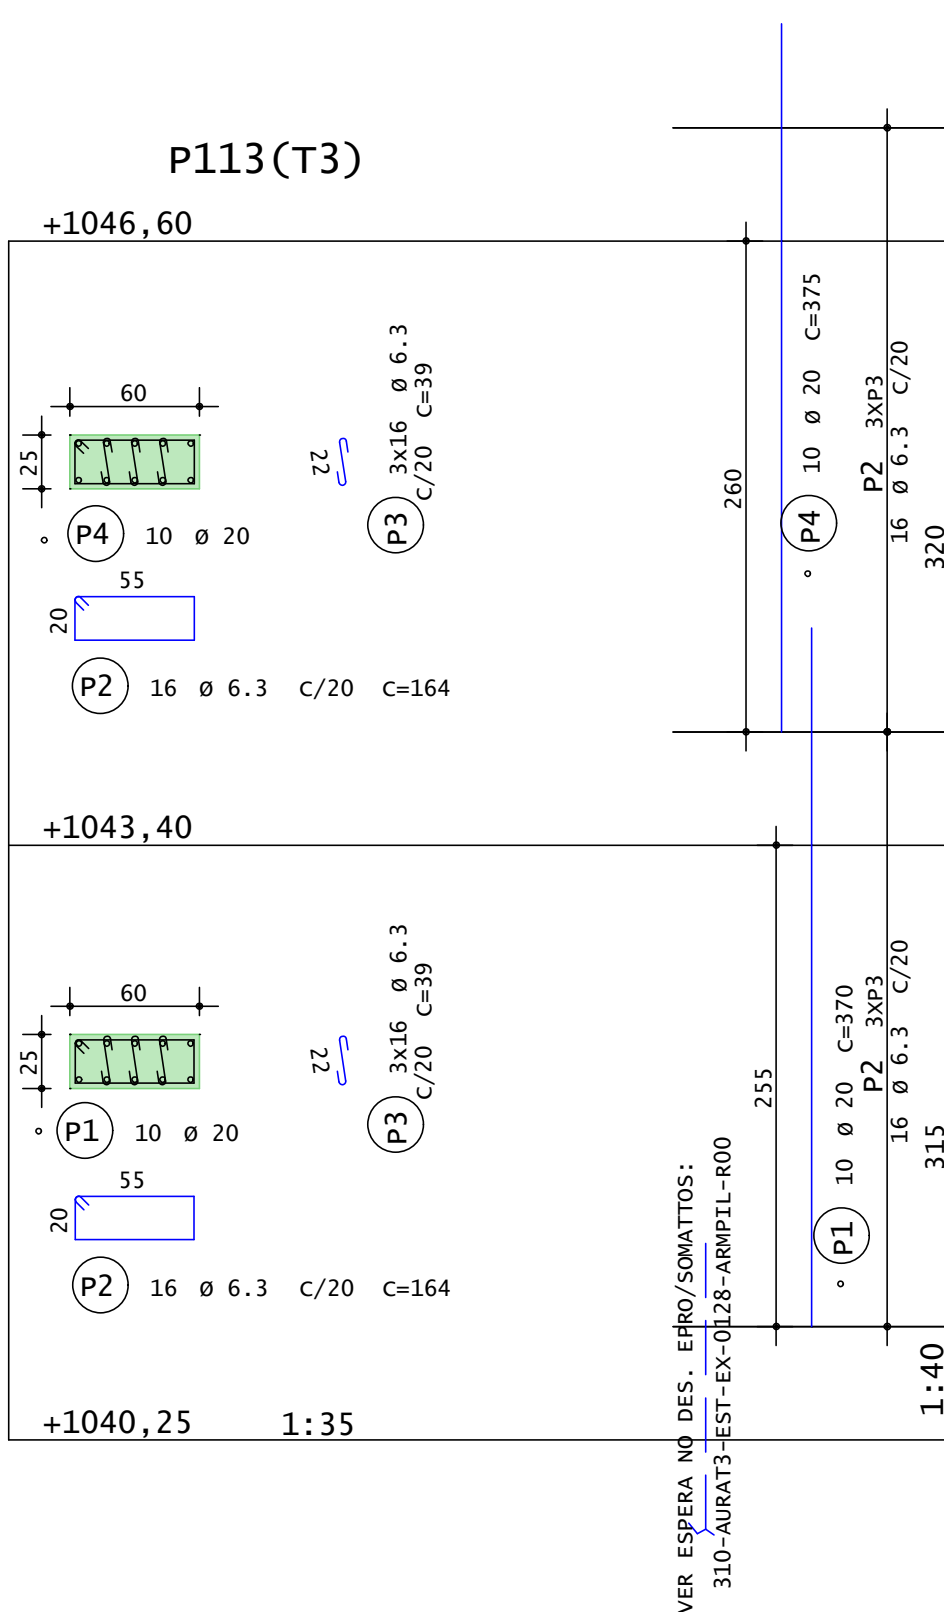
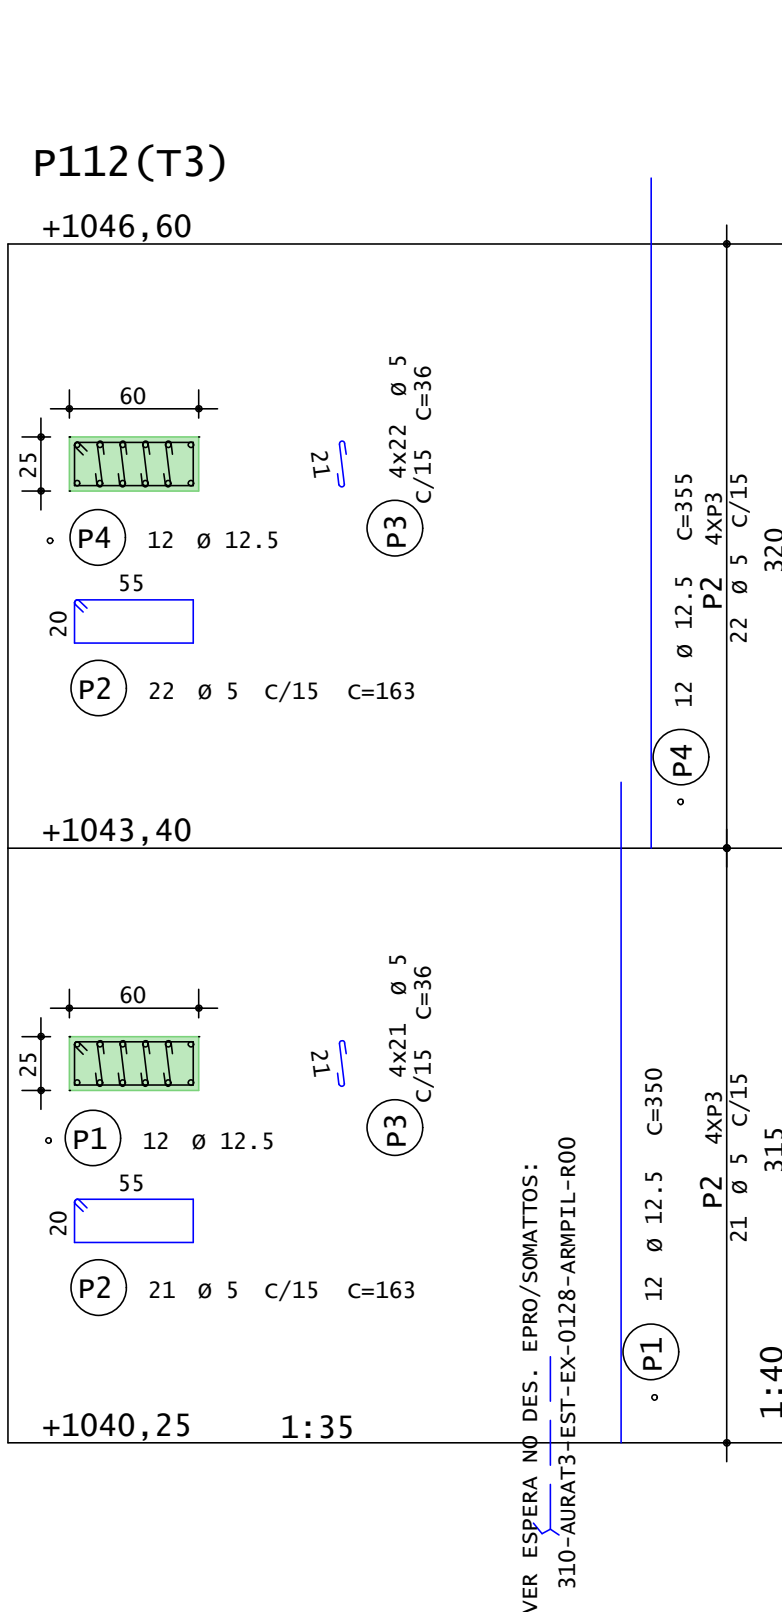


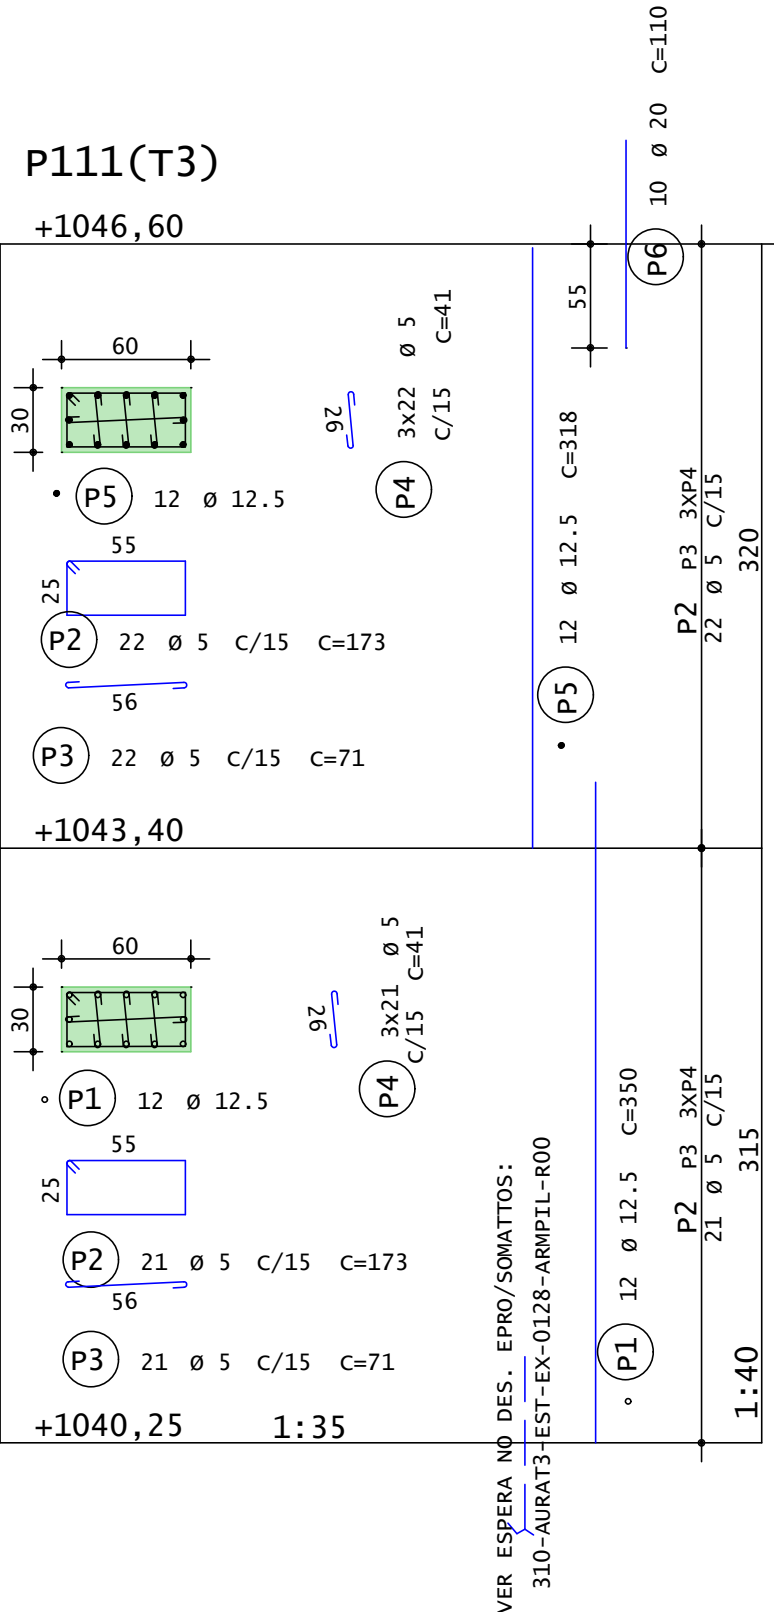

PROJETOS COMPLEMENTARES EM REFERÊNCIA:

- 1- FORMA DO 3o. SUBSOLO - TORRE 3: DES. EPRO/SOMATOS: 310-AURAE-EST-EX-0027-3SUBS3-R02;
- 2- FORMA DO 2o. SUBSOLO - TORRE 3: DES. EPRO/SOMATOS: 310-AURAE-EST-EX-0029-2SUBS3-R02;
- 3- FORMA DO 1o. SUBSOLO - TORRE 3: DES. EPRO/SOMATOS: 310-AURAE-EST-EX-0031-1SUBS3-R02;

NORMAS ATENDIDAS

- 1- NBR 6118/2023: PROJETO DE ESTRUTURAS DE CONCRETO;
- 2- NBR 14931/2004: EXECUÇÃO DE ESTRUTURAS DE CONCRETO - PROCEDIMENTO;
- 3- NBR 5674/2024: MANUTENÇÃO DE EDIFICAÇÕES-REQUISITOS PARA O SISTEMA DE GESTÃO E MANUTENÇÃO;
- 4- NBR 6120/2019: AÇÕES PARA CÁLCULO DE ESTRUTURA DE EDIFICAÇÕES;
- 5- NBR 6122/2019/eml:2022: PROJETO E EXECUÇÃO DE FUNDAÇÕES;
- 6- NBR 15575/2024: EDIFICAÇÕES HABITACIONAIS - DESEMPENHO;
- 7- NBR 6123/2023: FORÇAS DEVIDAS AO VENTO EM EDIFICAÇÕES;
- 8- NBR 15200/2024: PROJETO DE ESTRUTURAS DE CONCRETO EM SITUAÇÃO DE INCÊNDIO;
- 9- NBR 17170/2022: EDIFICAÇÕES - GARANTIAS - PRAZOS RECOMENDADOS E DIRETRIZES;

NOTAS GERAIS:

- 1- COTAS EM CENTÍMETRO, NÍVEIS EM METRO;
- 2- CONCRETO ESTRUTURAL:
 - FCK >= 40,0 MPa;
 - FATOR ÁGUA/CEMENTO (A/C) <= 0,60
 - CONSUMO MÍNIMO DE CIMENTO = 280 kg/m³;
 - TEMPO DE CURA, CONFORME CONDIÇÕES CLIMÁTICAS, MÍNIMO DE 7 (SETE) DIAS;
- 3- MÓDULO DE ELASTICIDADE INICIAL DO CONCRETO NBR 6118/2023;
Ec1 = 5600√FCK (DADOS EM MPa) - CxE=1,0 PARA GRANITO E GNATISSE:
PARA FCK >= 40,0 MPa - Ec1 = 33130 MPa;
- 4- CORRIMENTOS = 2,5 CM;
- 5- AÇOS CA 50 e CA 60;

05			
04			
03			
02			
01			
00	EMISSION INICIAL		
Nº	HISTÓRICO	REVISÕES	RESPONSÁVEL

PROPRIETÁRIO:
SOMATOS PATRIMAR Q.40 EMPREEND. IMOBILIÁRIOS SPE LTDA
CNPJ: 42.306.807/0001-05

AUTOR DO PROJETO:
TORRES MIRANDA ARQUITETURA E CONSULTORIA LTDA
CAU: 8447-6

RESPONSÁVEL TÉCNICO EXECUÇÃO:
BERNARDO IMPELLIZIERI SÁ MATOS
CREA: 82679/D MG

RESPONSÁVEL TÉCNICO PROJ. EXECUTIVO:
EPRO ENGENHARIA DE PROJETOS E CONSULTORIA S/C LTDA
CREA: 6154/MG

ENGENHEIRO COLABORADOR:
LUIZ RENATO DE LIMA
CREA: 26927/D

EMPREENHIMENTO:			
CÓDIGO: 310 - AURA - TORRE 3			
LOCAL:	RUA CEL. GABRIEL FELIPE FARIA, VILA DA SERRA - NOVA LIMA - MG	BAIRRO:	JARDINAVES
PROJETO:	PROJETO EXECUTIVO ESTRUTURAL		
CONTEÚDO:	ARMAÇÃO DOS PILARES DO NÍVEL +1040,25 a +1046,60		
ARQUIVO:	310-AURAT3-EST-EX-0145-ARMPIL-R00		
REVISÃO:	R00		
ESCALA:	INDICADA		
FOLHA:	145/		