
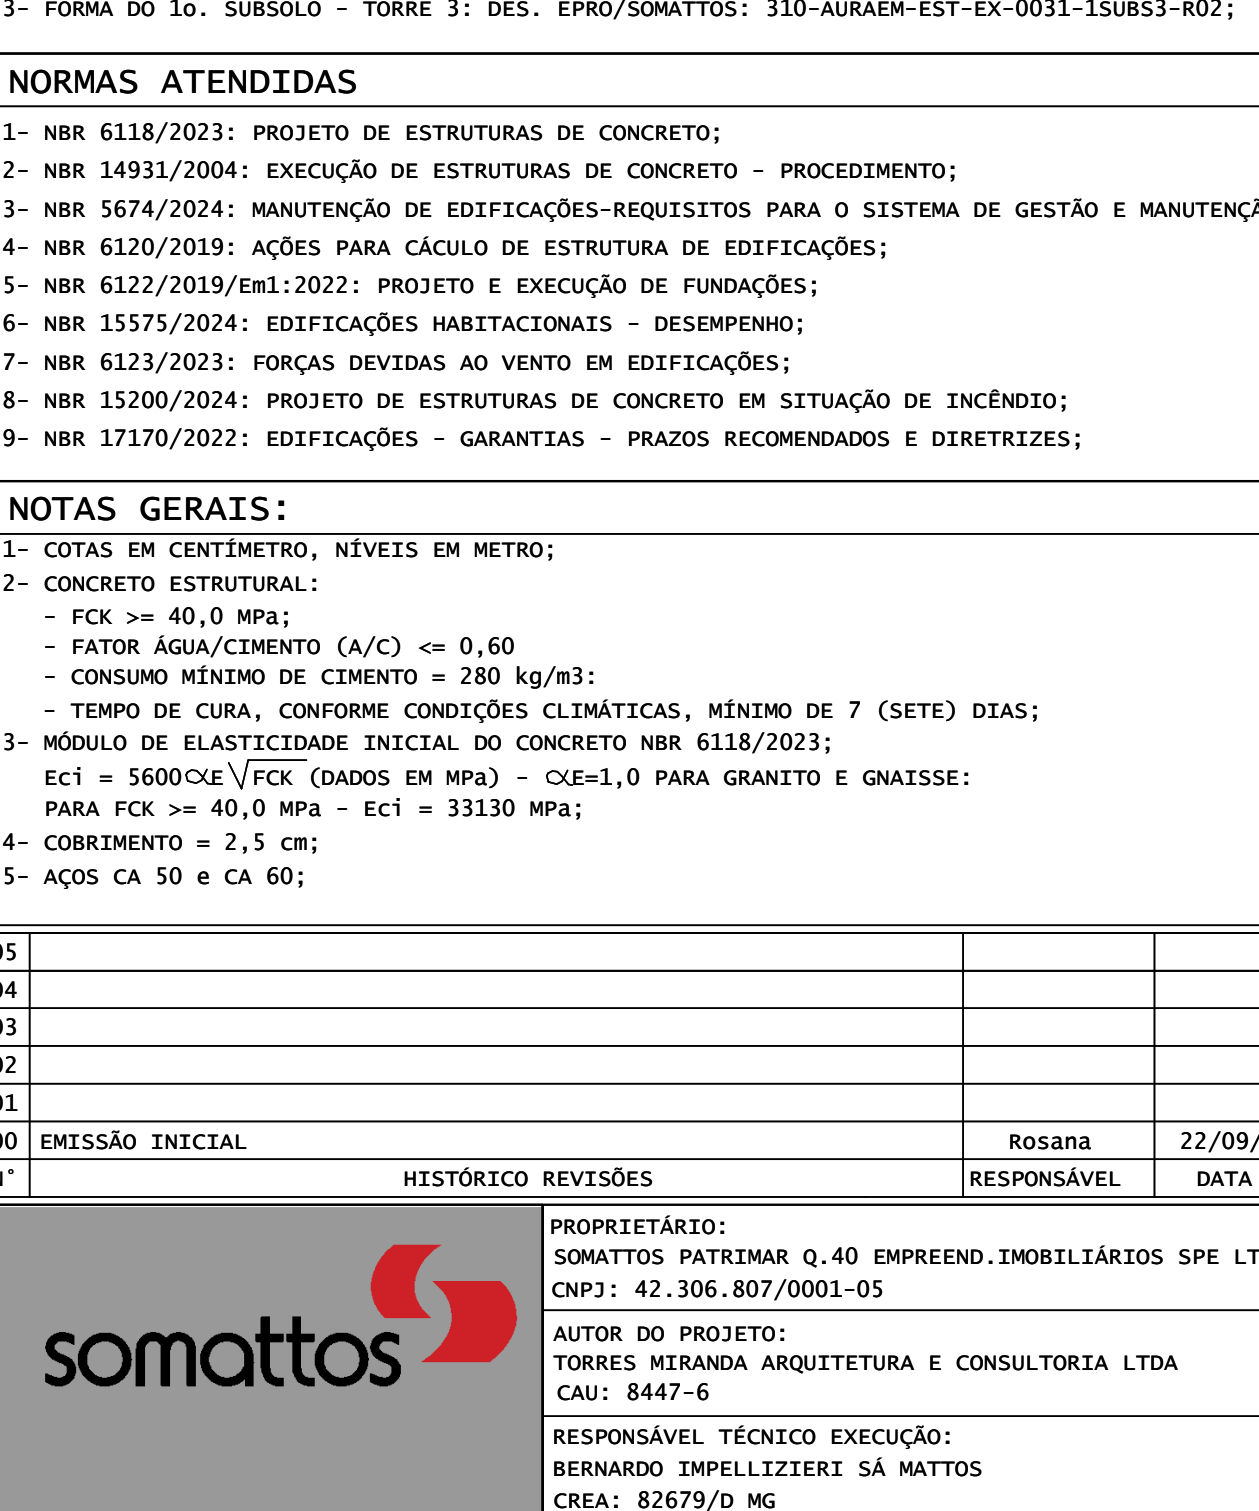
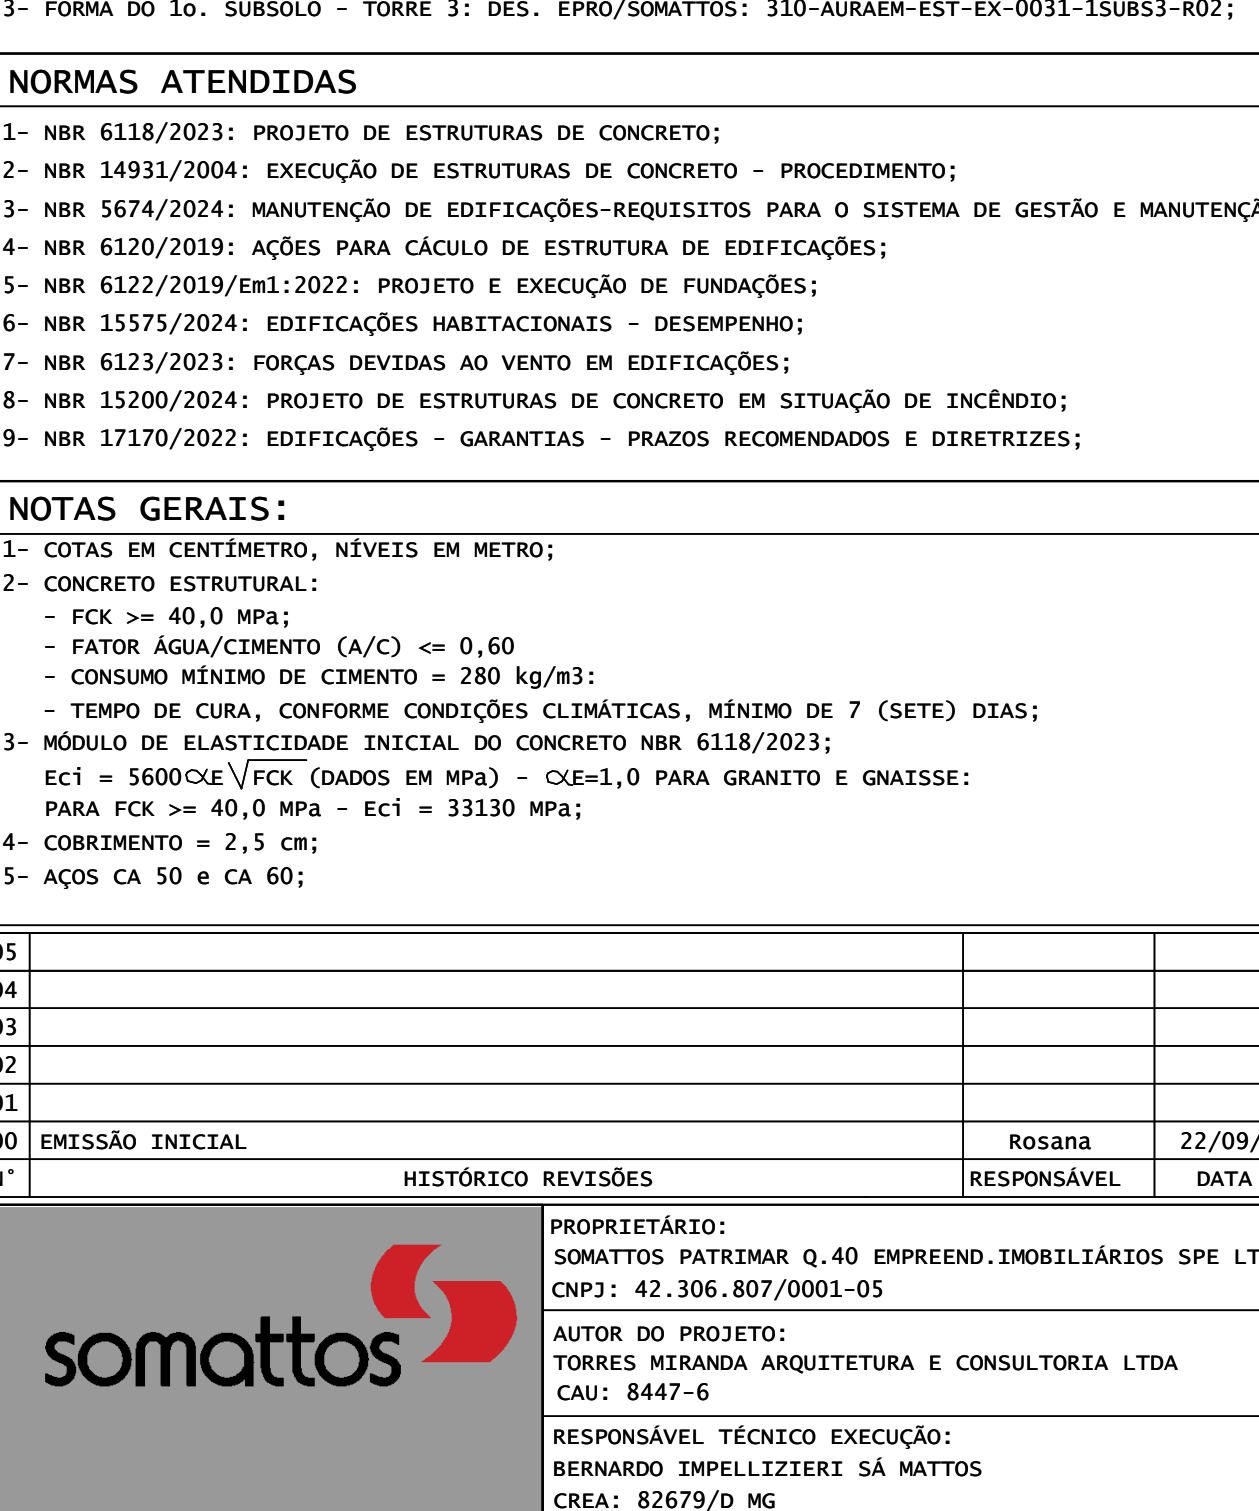
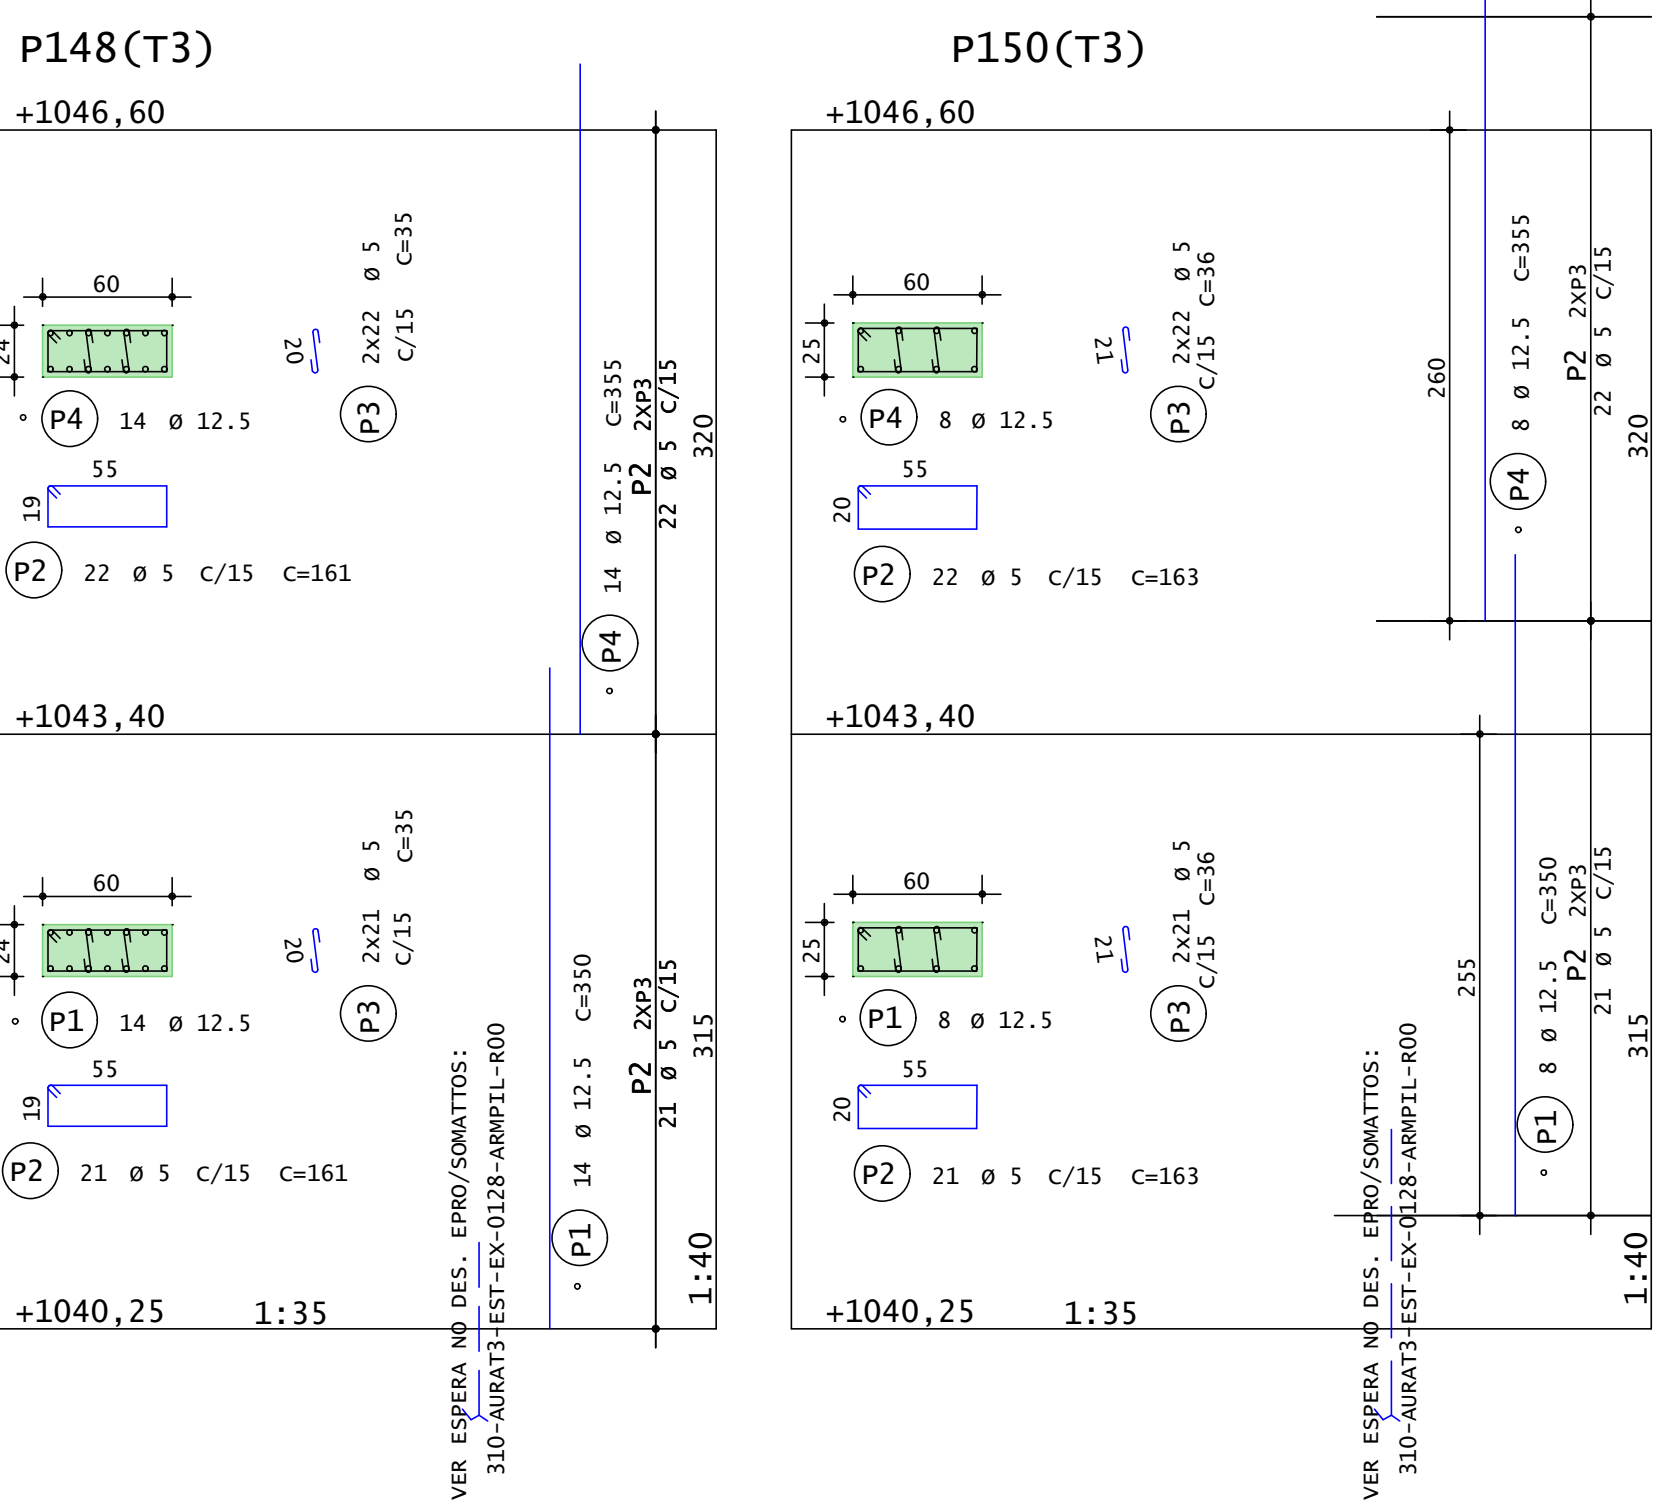
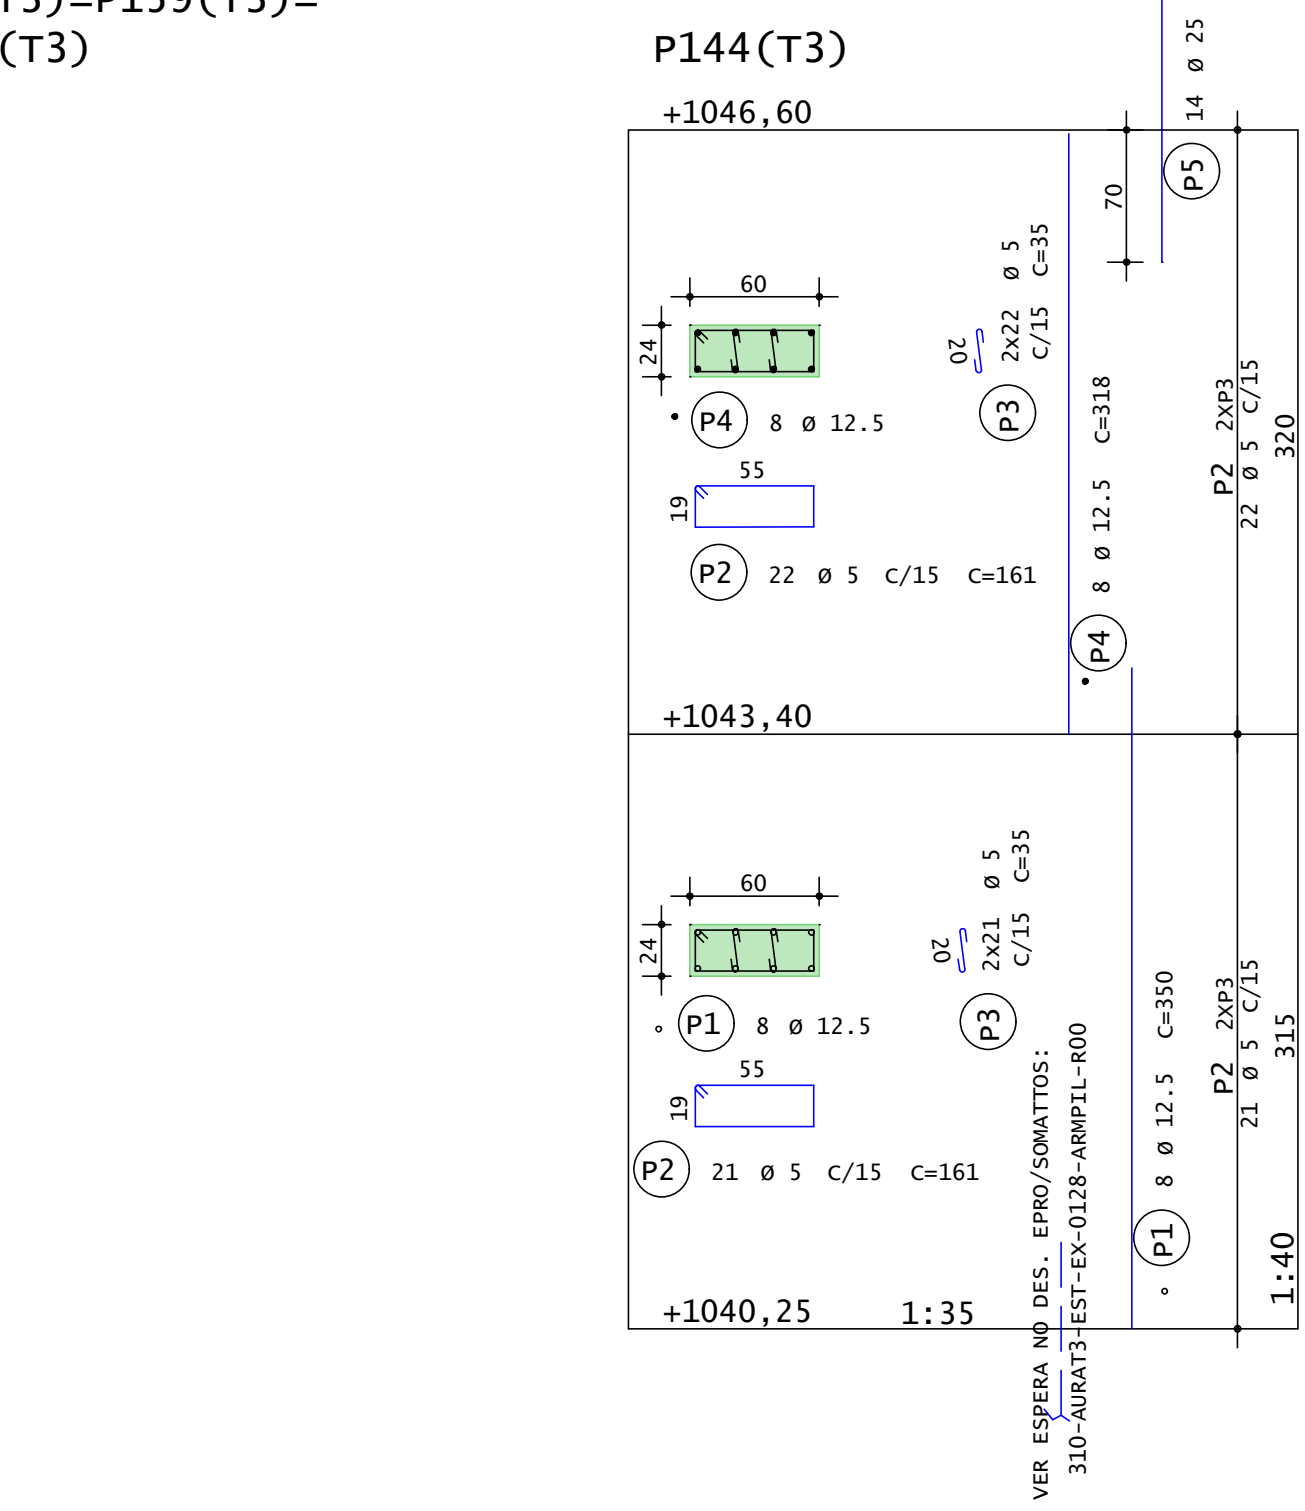
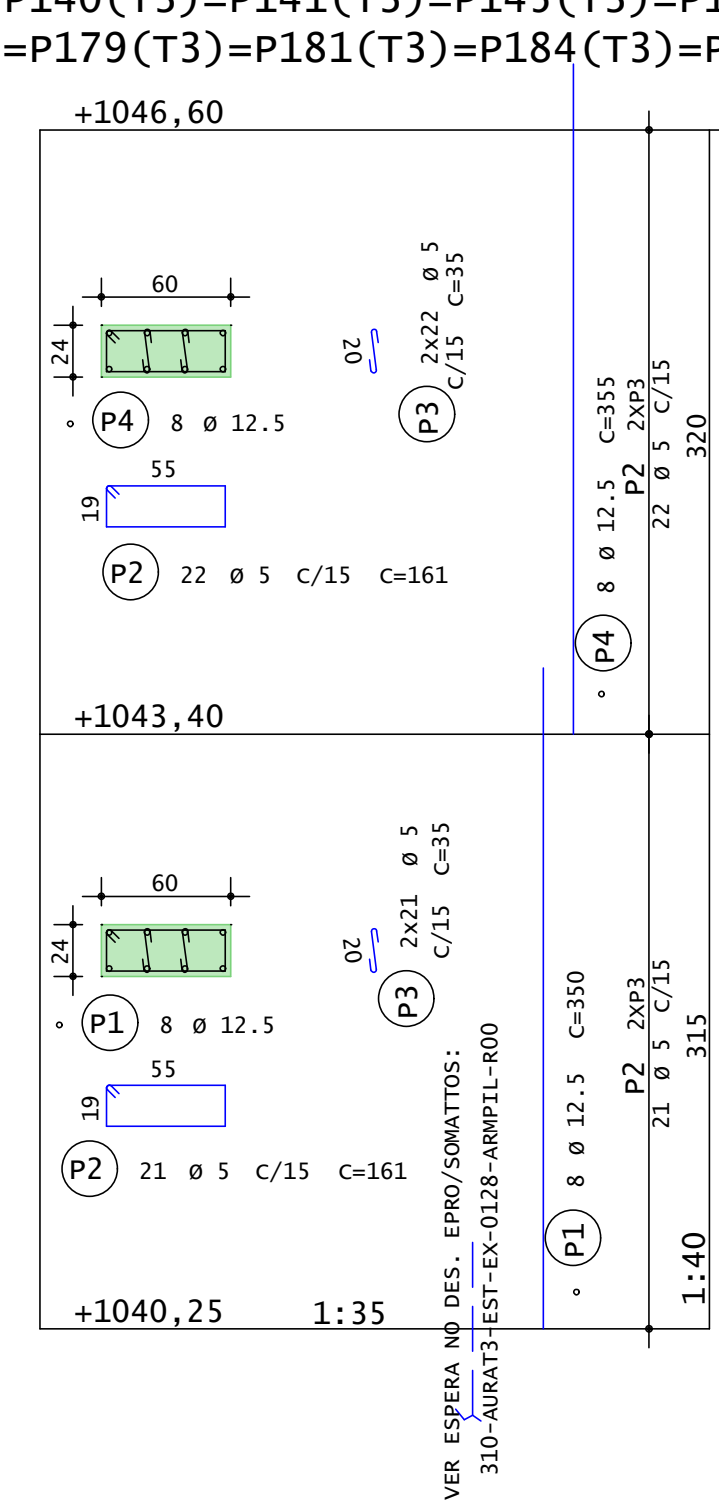
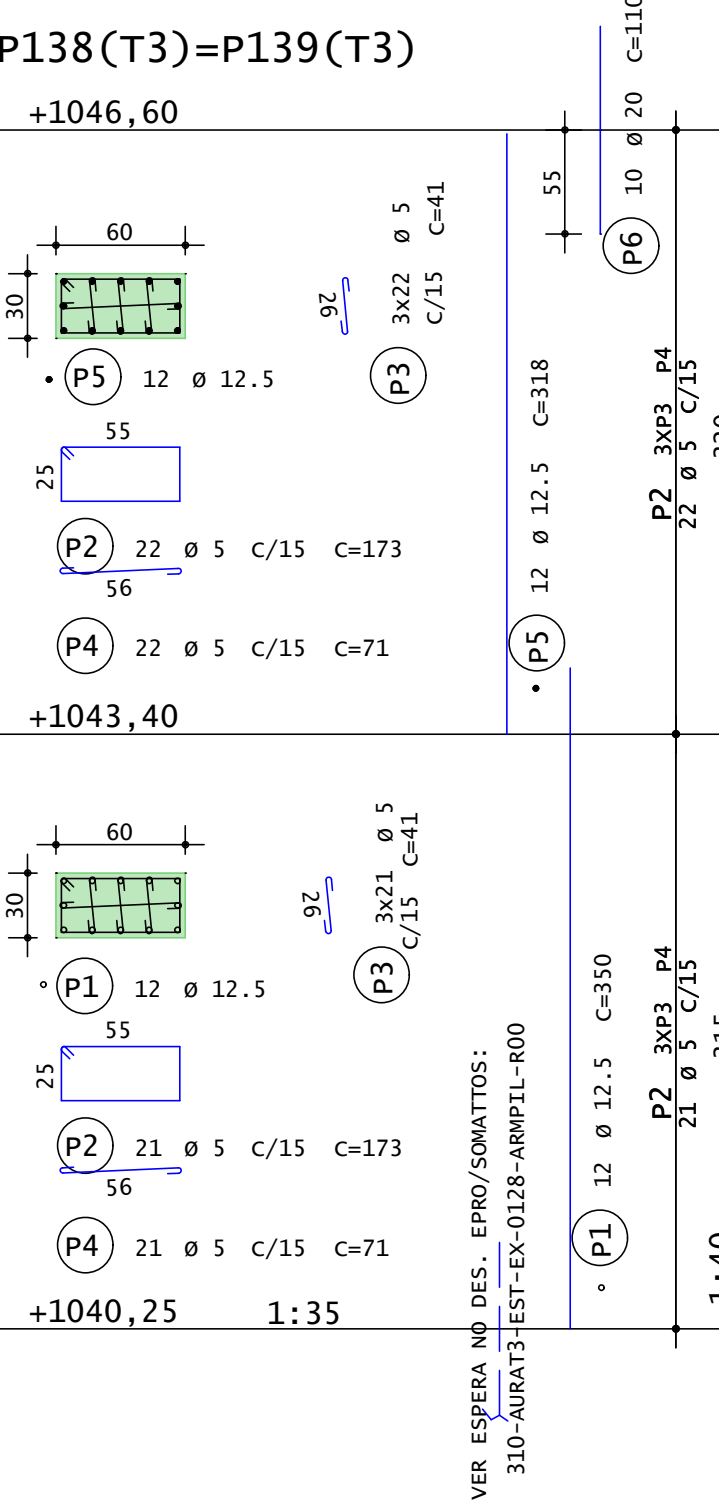
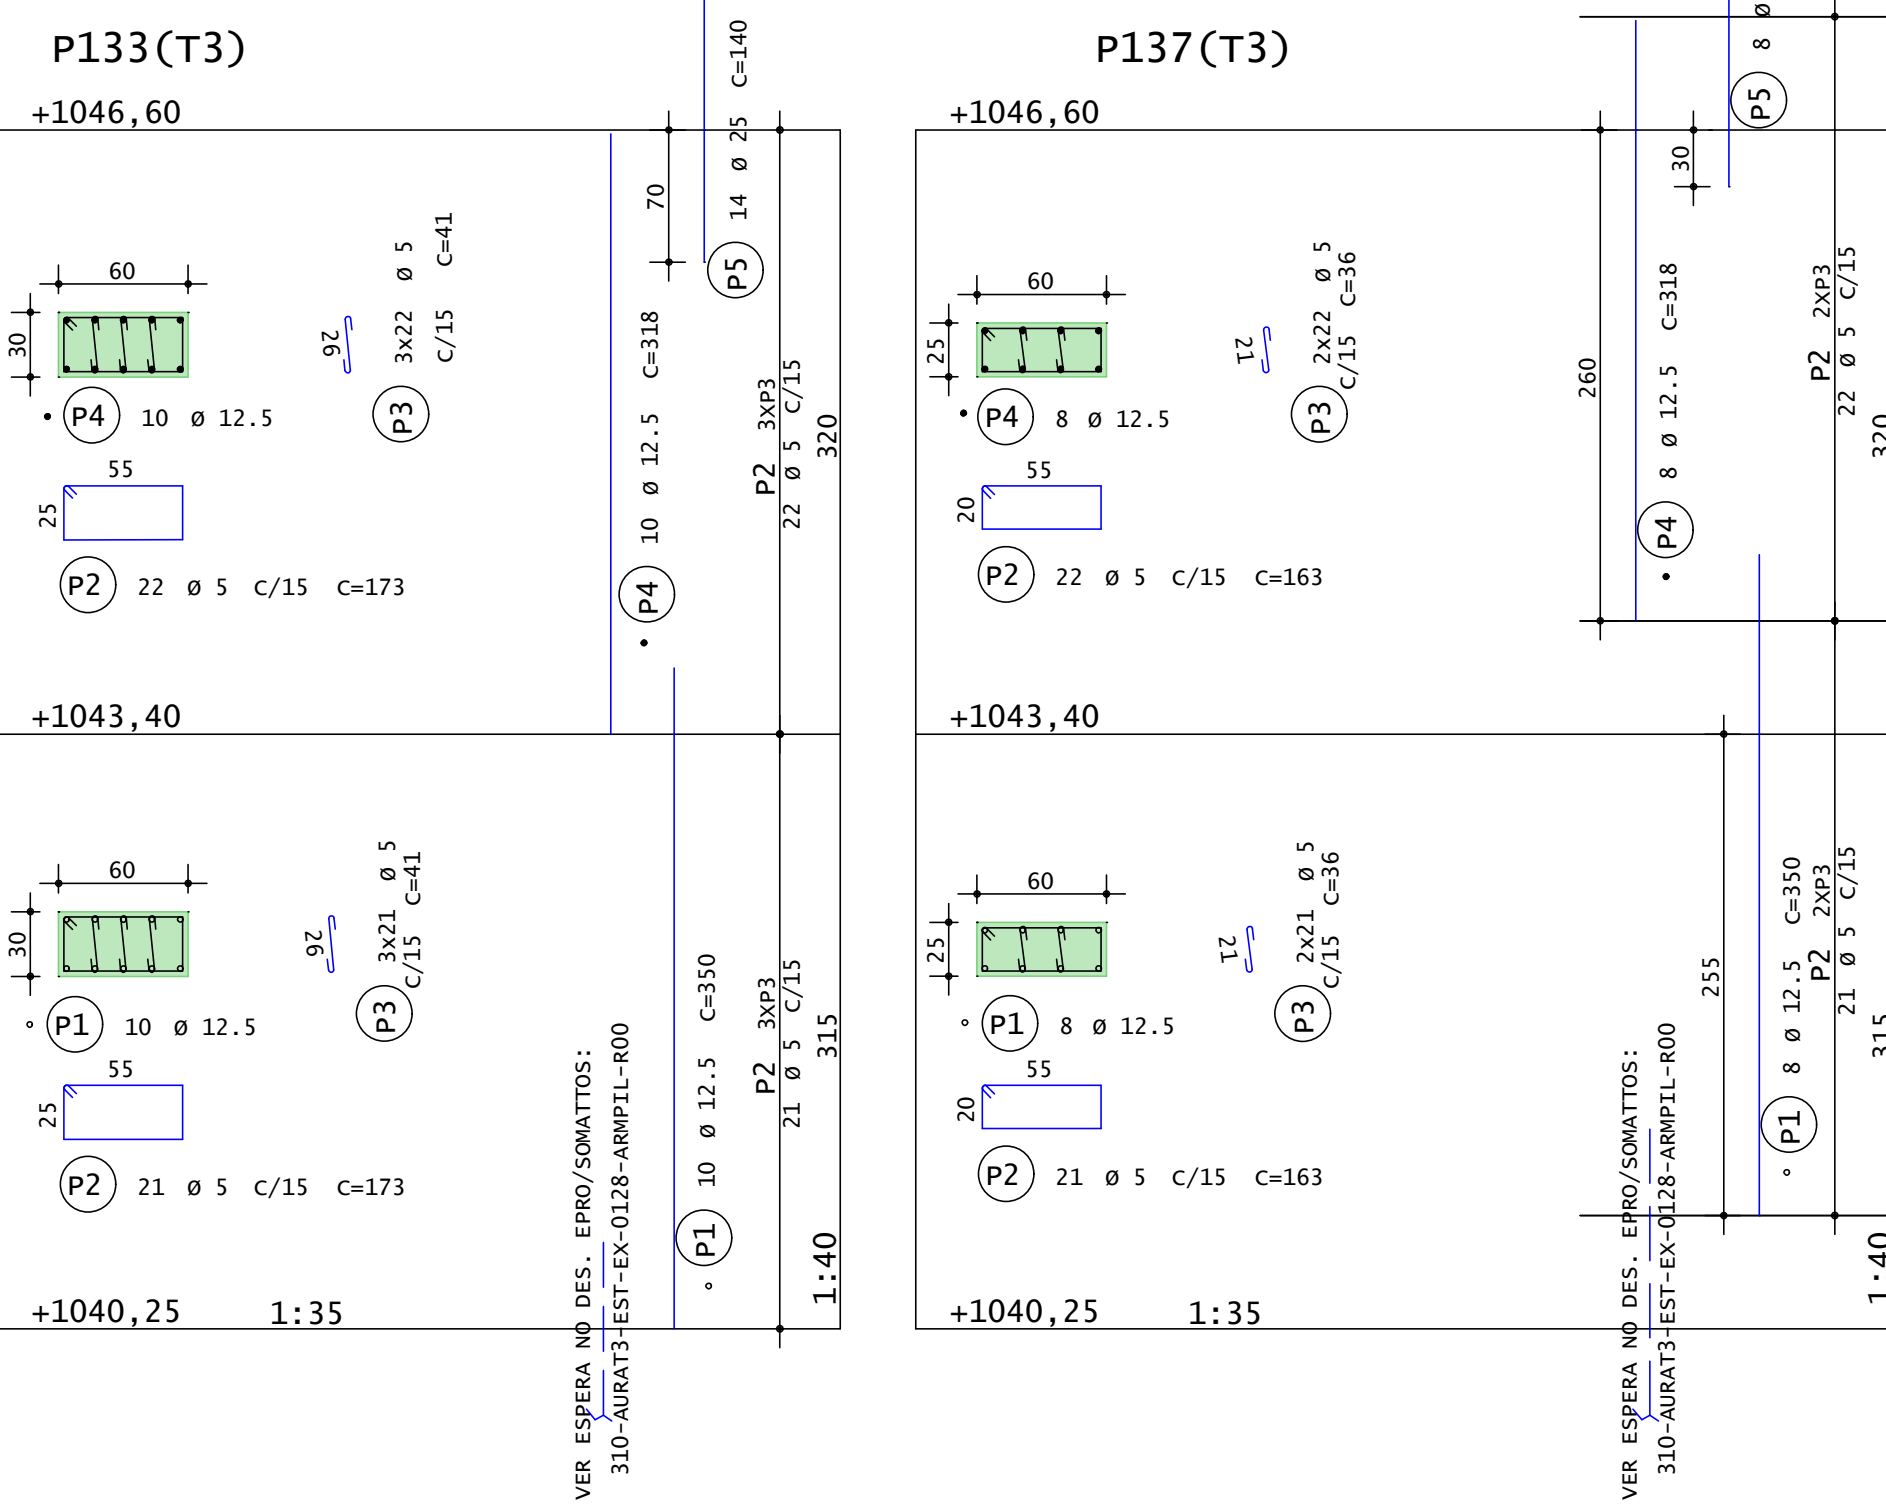
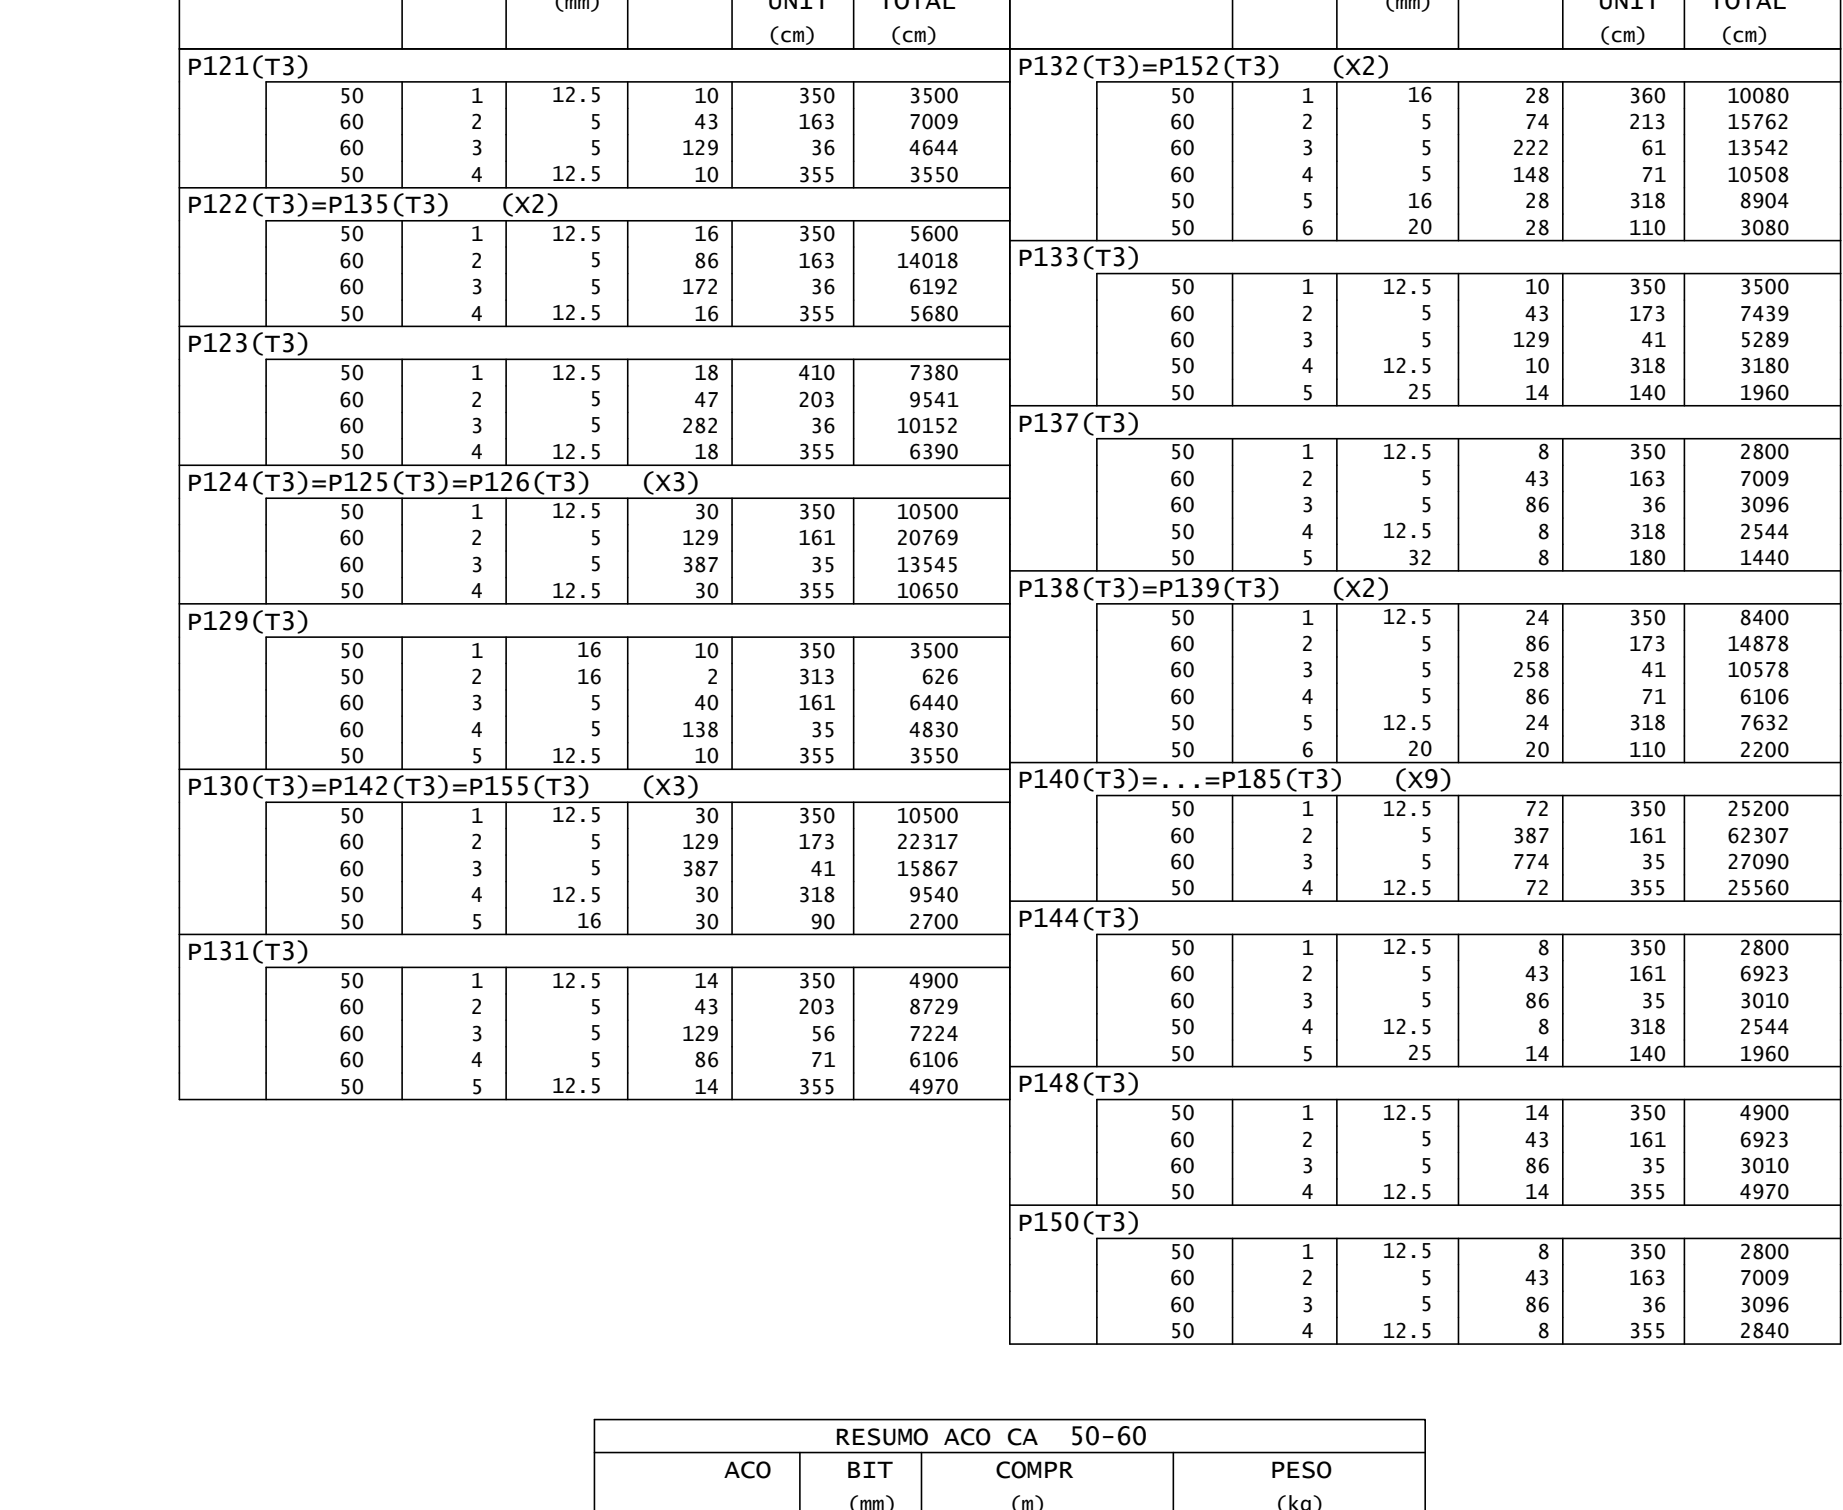
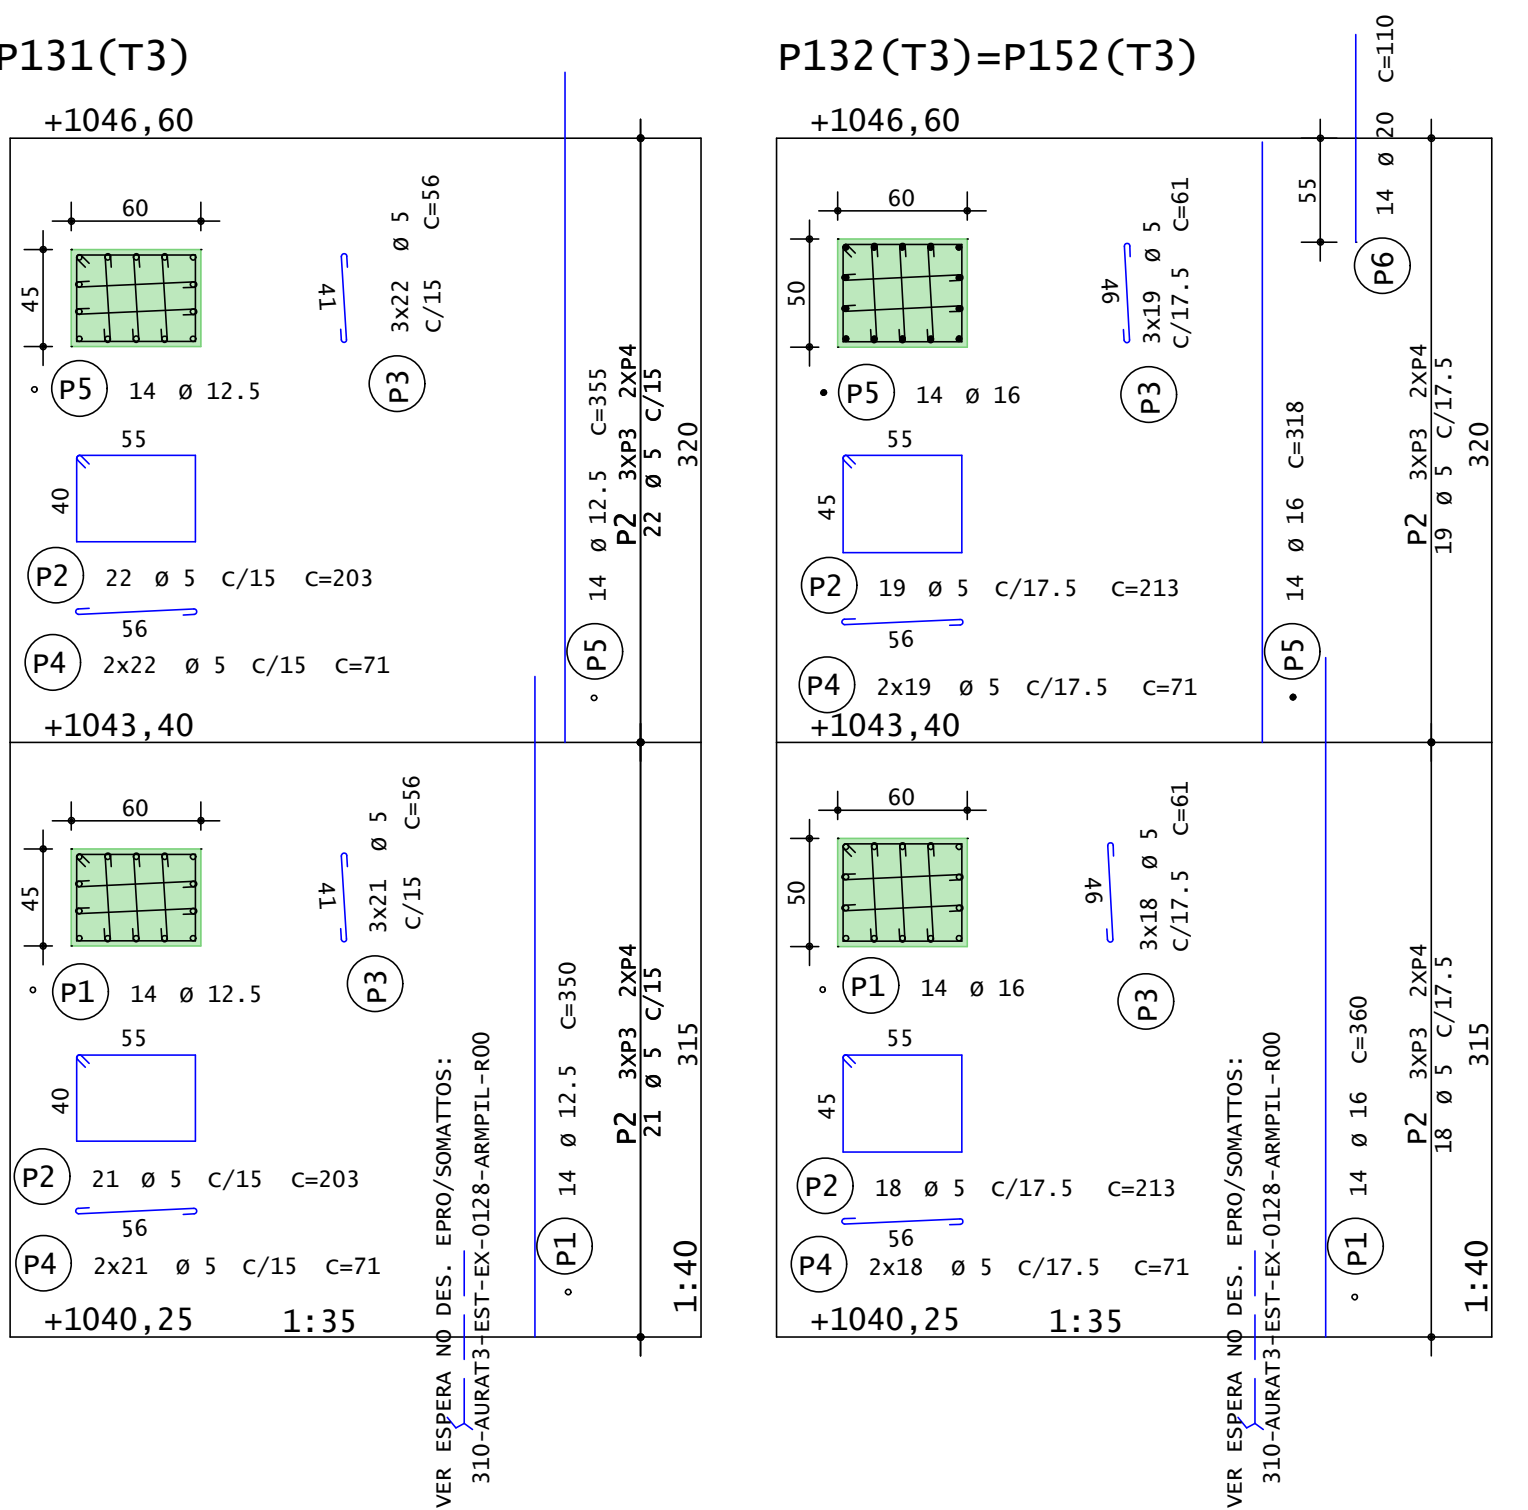
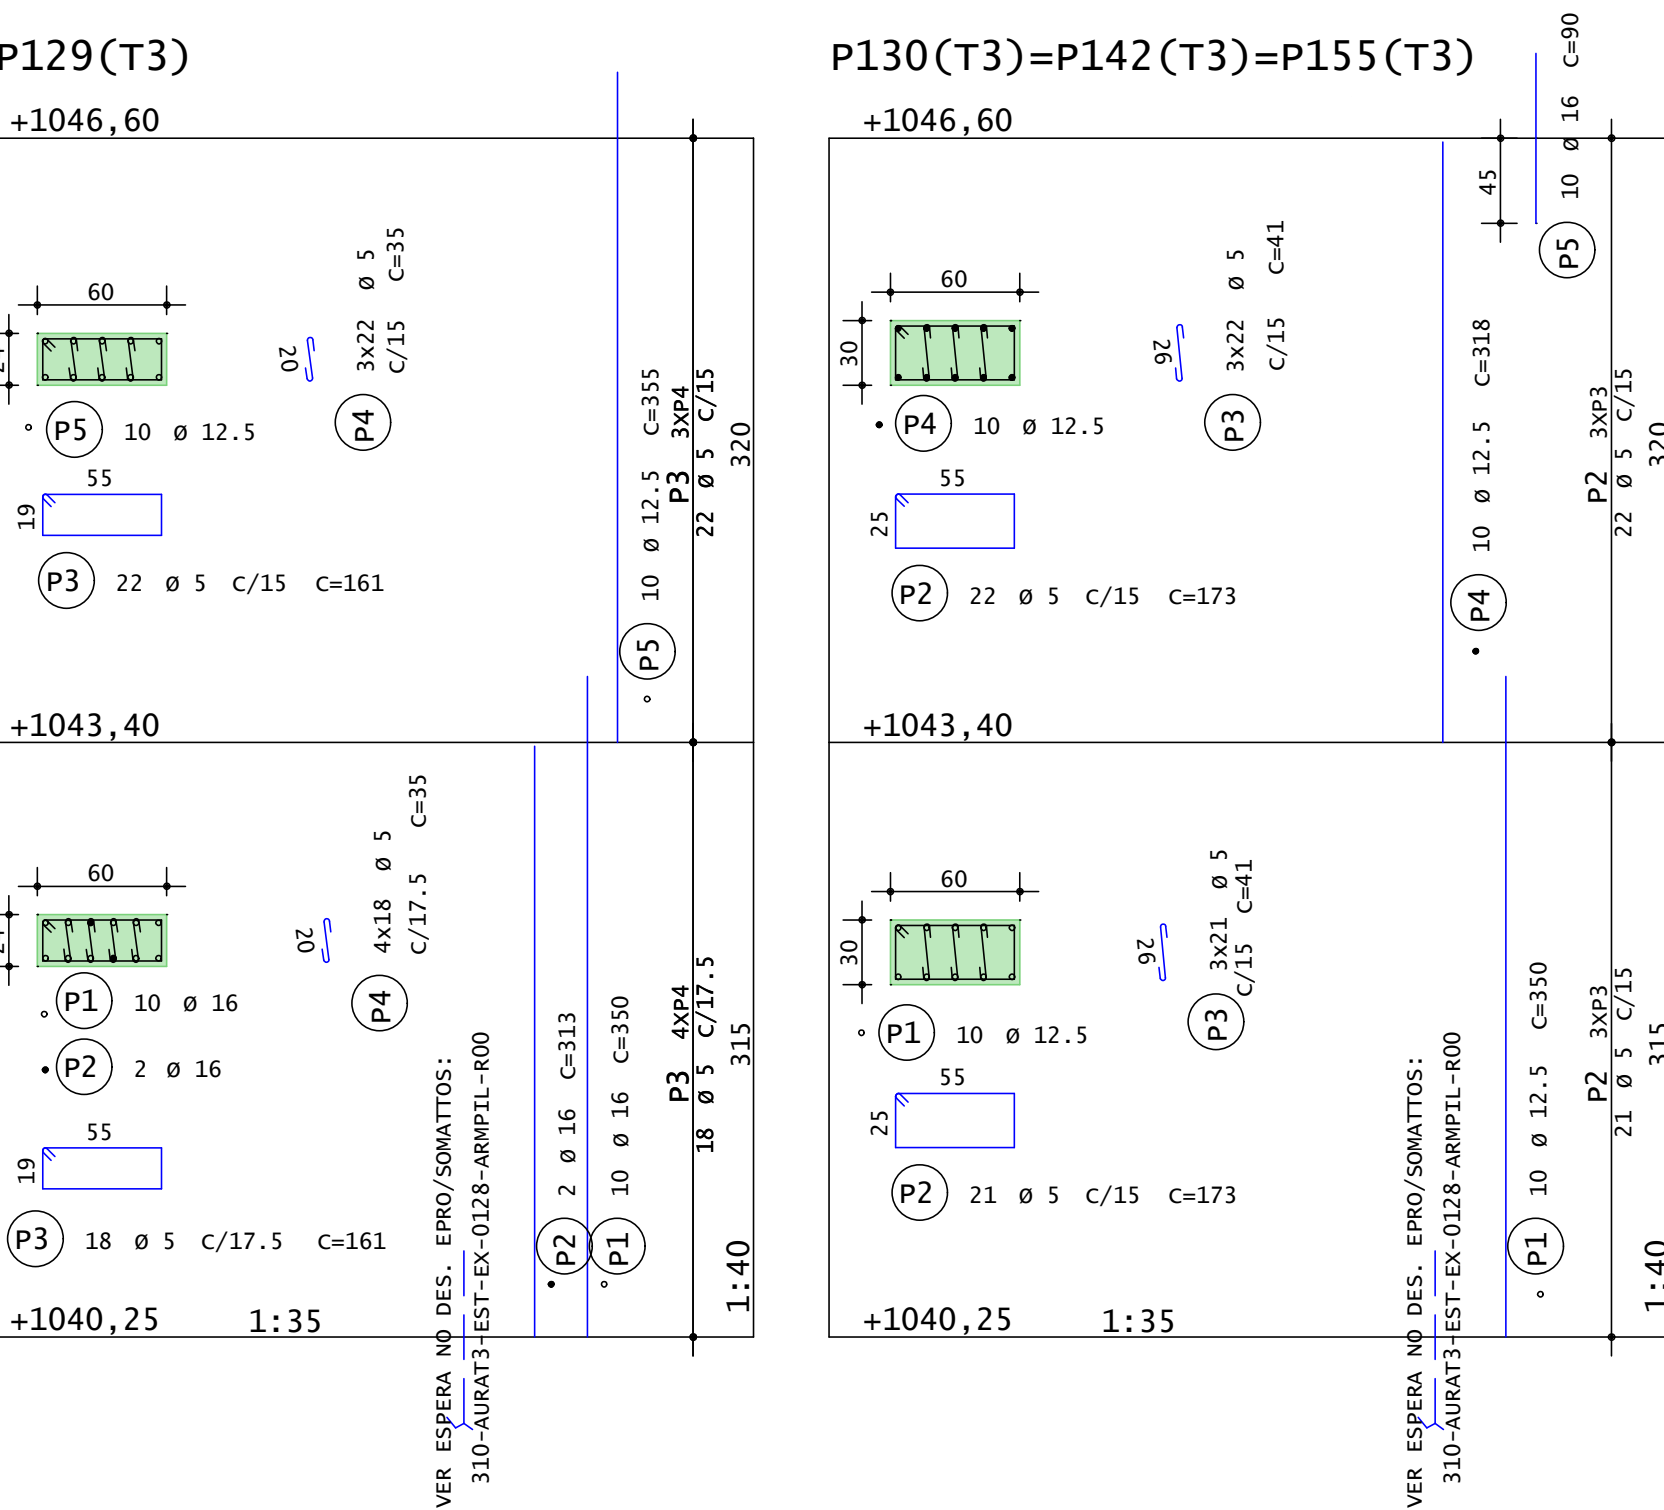
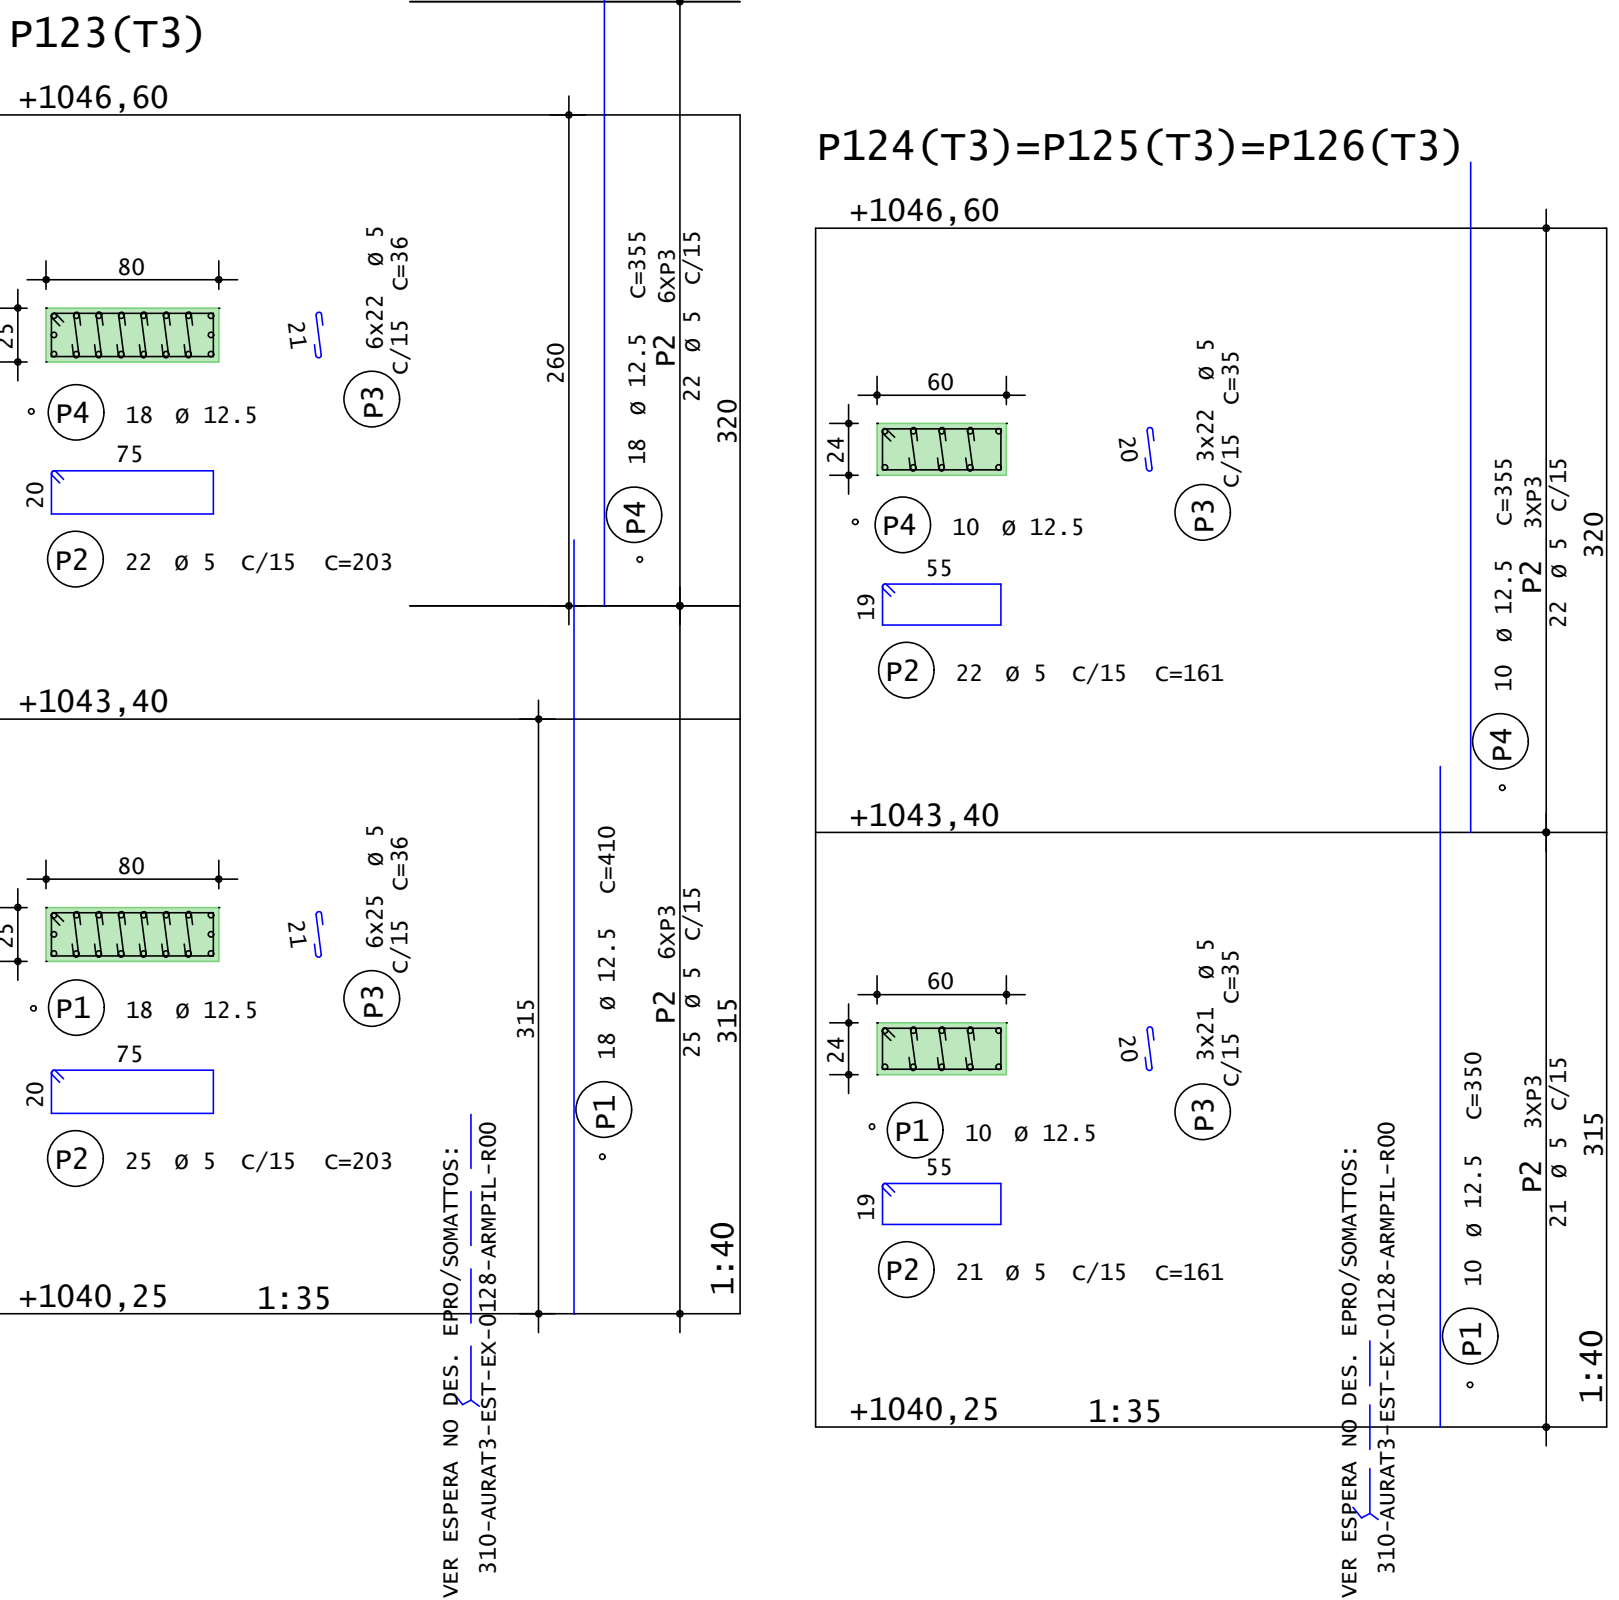


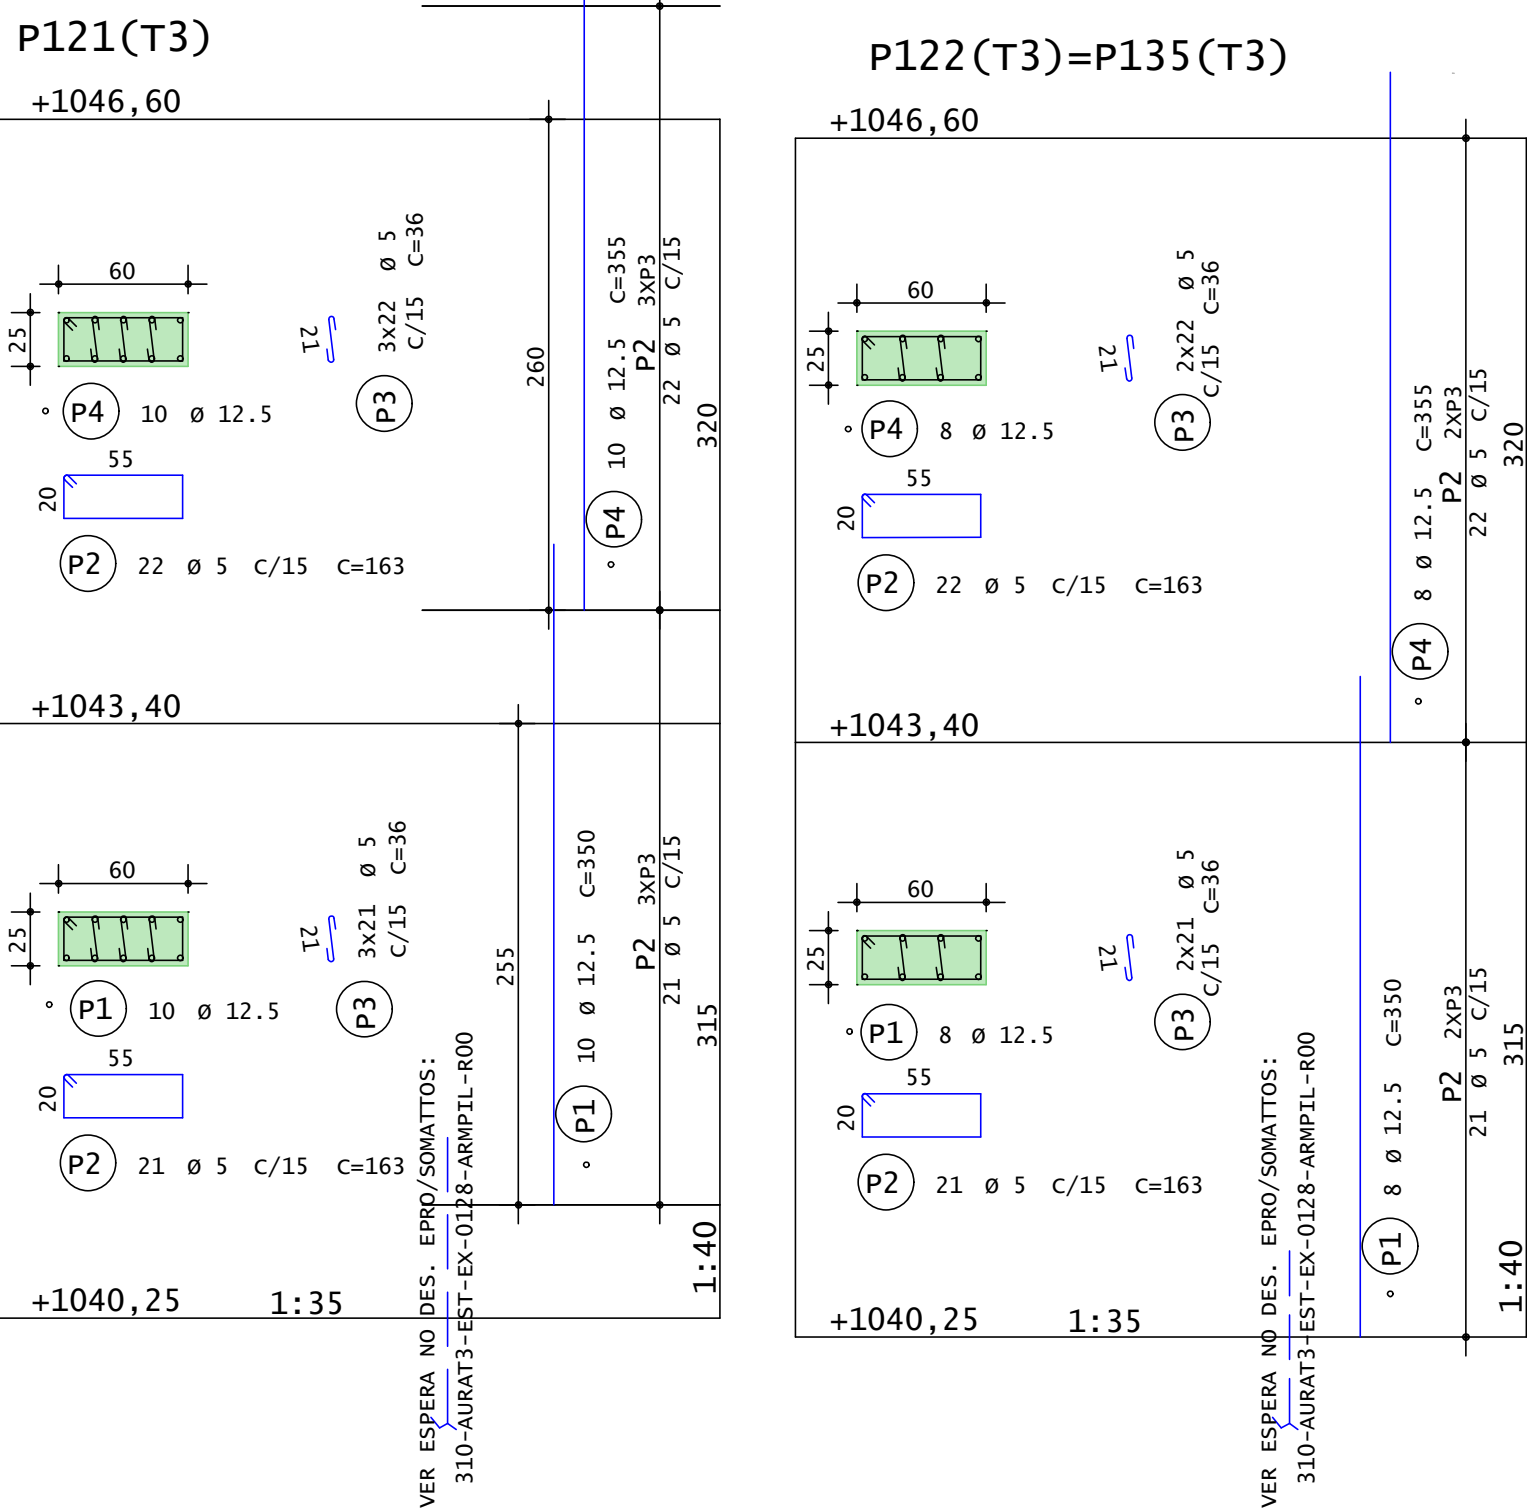

RESUMO ACO CA 50-60			
ACO	BIT	COMPR	PESO
(mm)	(mm)	(m)	(kg)
60	5	3710	571
50	12,5	1864	1795
50	16	258	407
50	20	53	130
50	25	39	151
50	32	14	91
Peso Total		60 =	571 kgf
Peso Total		50 =	2574 kgf

PROJETOS COMPLEMENTARES EM REFERÊNCIA:

1- FORMA DO 3o. SUBSOLO - TORRE 3: DES. EPRO/SOMATOS: 310-AURAE-EST-EX-0027-3SUBS3-R02;
2- FORMA DO 2o. SUBSOLO - TORRE 3: DES. EPRO/SOMATOS: 310-AURAE-EST-EX-0029-2SUBS3-R02;
3- FORMA DO 1o. SUBSOLO - TORRE 3: DES. EPRO/SOMATOS: 310-AURAE-EST-EX-0031-1SUBS3-R02;

NORMAS ATENDIDAS

1- NBR 6118/2023: PROJETO DE ESTRUTURAS DE CONCRETO;
2- NBR 14931/2004: EXECUÇÃO DE ESTRUTURAS DE CONCRETO - PROCEDIMENTO;
3- NBR 5674/2024: MANUTENÇÃO DE EDIFICAÇÕES-REQUISITOS PARA O SISTEMA DE GESTÃO E MANUTENÇÃO;
4- NBR 6120/2019: AÇÕES PARA CÁLCULO DE ESTRUTURA DE EDIFICAÇÕES;
5- NBR 6122/2019/EN1:2022: PROJETO E EXECUÇÃO DE FUNDAÇÕES;
6- NBR 15575/2024: EDIFICAÇÕES HABITACIONAIS - DESEMPENHO;
7- NBR 6123/2023: FORÇAS DEVIDAS AO VENTO EM EDIFICAÇÕES;
8- NBR 15200/2024: PROJETO DE ESTRUTURAS DE CONCRETO EM SITUAÇÃO DE INCÊNDIO;
9- NBR 17170/2022: EDIFICAÇÕES - GARANTIAS - PRAZOS RECOMENDADOS E DIRETRIZES;

NOTAS GERAIS:

1- COTAS EM CENTÍMETRO, NÍVEIS EM METRO;
2- CONCRETO ESTRUTURAL:
- FCK >= 40,0 MPa;
- FATOR ÁGUA/CEMENTO (A/C) <= 0,60
- CONSUMO MÍNIMO DE CIMENTO = 280 kg/m³;
- TEMPO DE CURA, CONFORME CONDIÇÕES CLIMÁTICAS, MÍNIMO DE 7 (SETE) DIAS;
3- MÓDULO DE ELASTICIDADE INICIAL DO CONCRETO NBR 6118/2023;
Ec1 = 5600√FCK (DADOS EM MPa) - Cxk=1,0 PARA GRANITO E GNATISSE:
PARA FCK >= 40,0 MPa - Ec1 = 33130 MPa;
4- COBRIMENTO = 2,5 CM;
5- AÇOS CA 50 e CA 60;

05			
04			
03			
02			
01			
00			
EMISSION INICIAL		Rosana	22/09/25
N°	HISTÓRICO	REVISÕES	RESPONSÁVEL DATA

PROPRIETÁRIO:
SOMATOS PATRIMAR Q.40 EMPREND.IMOBILIÁRIOS SPE LTDA
CNPJ: 42.306.807/0001-05

AUTOR DO PROJETO:
TORRES MIRANDA ARQUITETURA E CONSULTORIA LTDA
CAU: 8447-6

RESPONSÁVEL TÉCNICO EXECUÇÃO:
BERNARDO IMPELLIZZIERI SÁ MATTOS
CREA: 82679/D MG

RESPONSÁVEL TÉCNICO PROJ. EXECUTIVO:
EPRO ENGENHARIA DE PROJETOS E CONSULTORIA S/C LTDA
CREA: 6154/MG

ENGENHEIRO COLABORADOR:
LUIZ RENATO DE LIMA
CREA: 26927/D

EMPREENDIMENTO: 310 - AURA - TORRE 3			
LOCAL: RUA CEL. GABRIEL FELIPE FARIA, VILA DA SERRA - NOVA LIMA - MG		BAIRRO: JARDINAVES	
PROJETO: PROJETO EXECUTIVO ESTRUTURAL		DATA 1a. EMISSÃO: 22/09/2025	
CONTEÚDO: ARMAÇÃO DOS PILARES DO NÍVEL +1040,25 a +1046,60 3o. SUBSOLO AO 1o. SUBSOLO (5a. PARTE)		REVISÃO: ROO	
ARQUIVO: 310-AURAT3-EST-EX-0146-AMPIL-R00		ESCALA: INDICADA	
		FOLHA: 146/	