


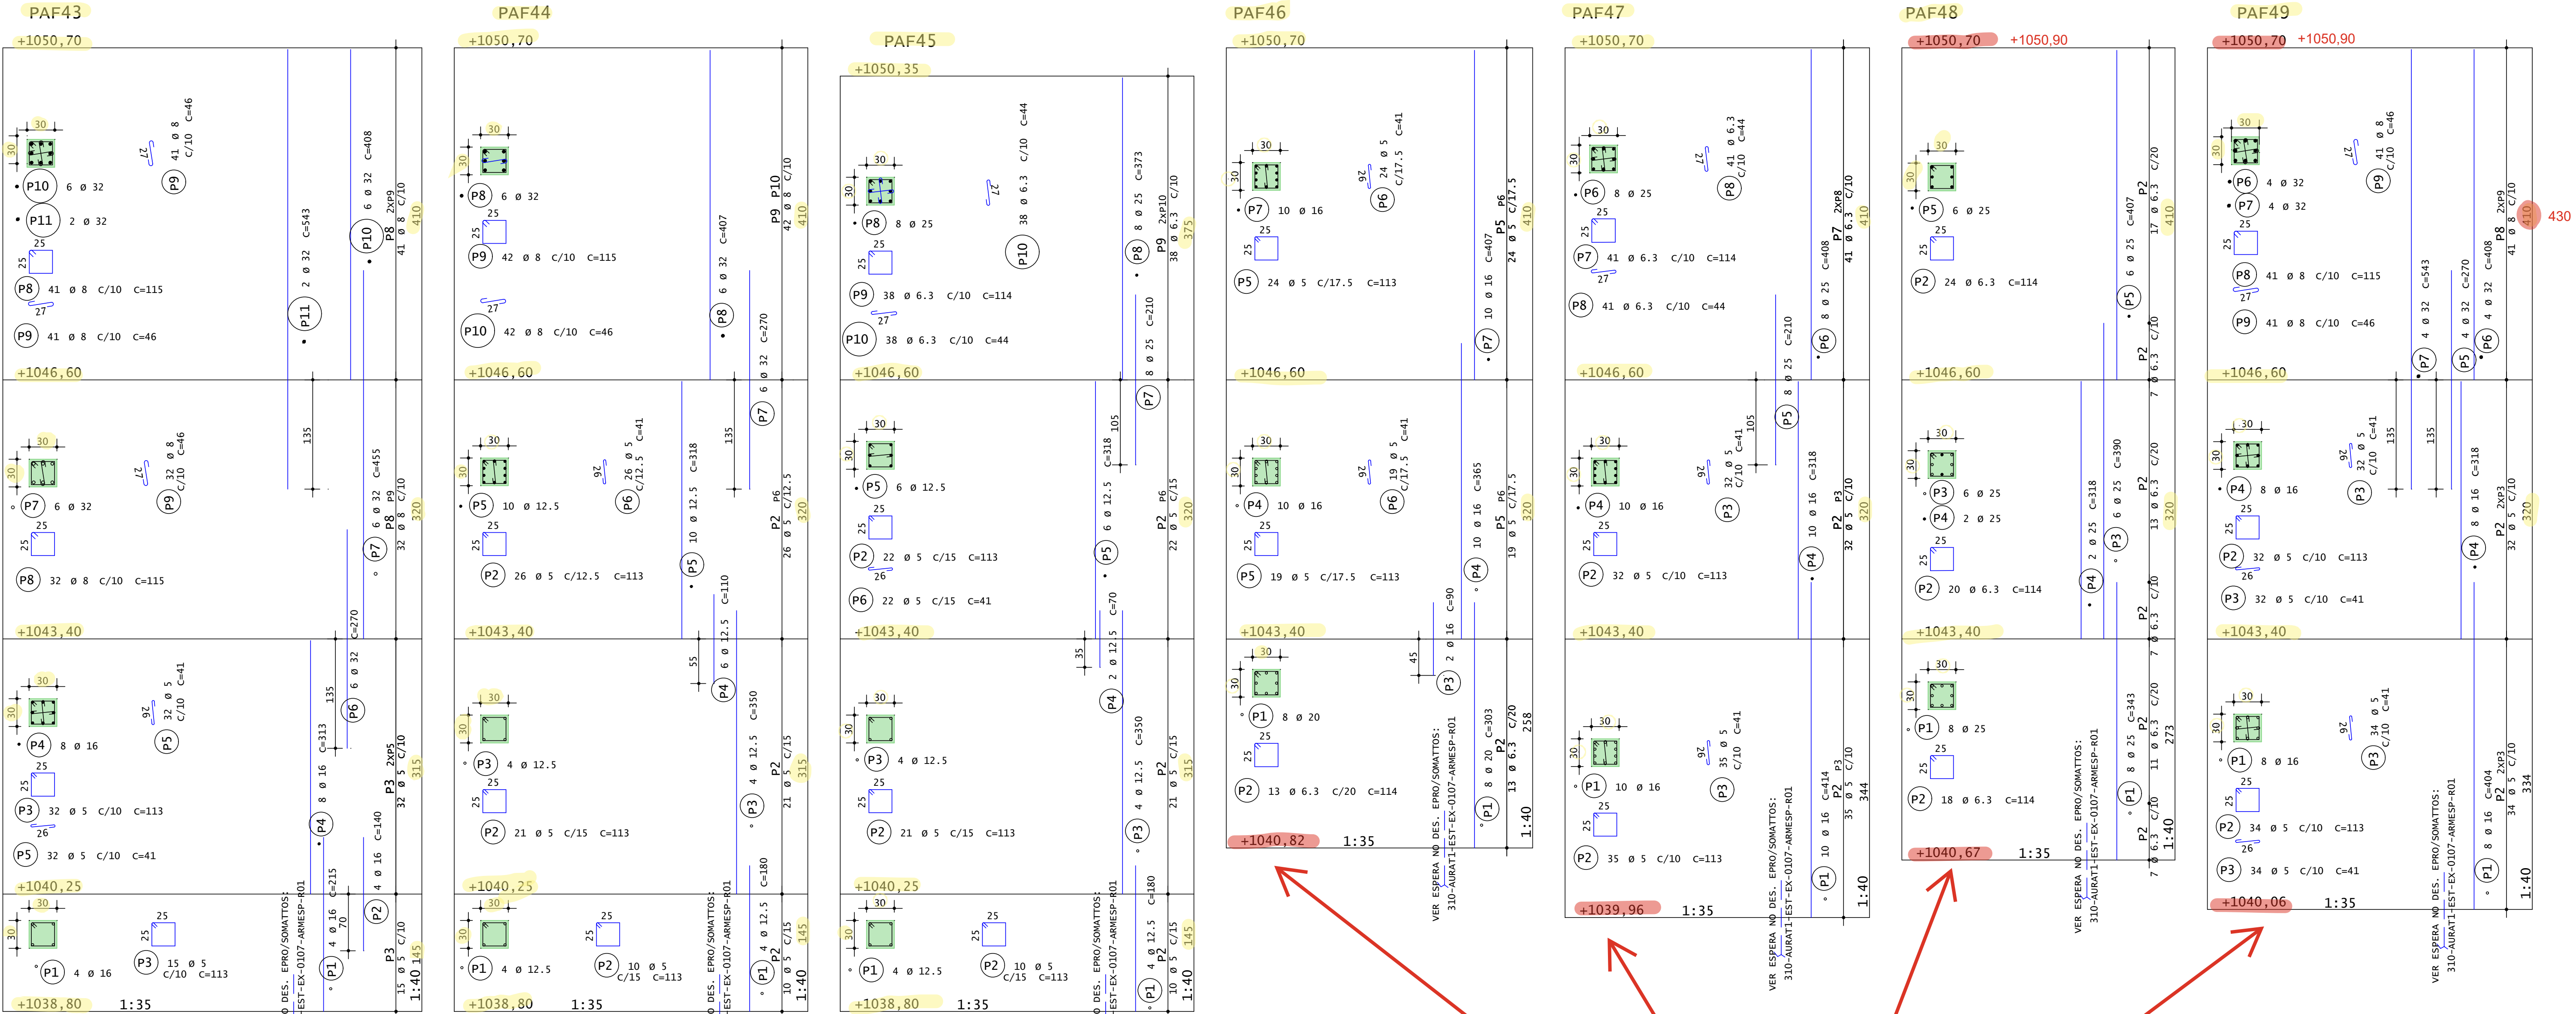

INCOMPATÍVEL COM A FORMA

ACO	POS	BIT (mm)	QUANT	COMPRIMENTO	
				UNIT (cm)	TOTAL (cm)
PAF43	50	1	16	4	215
	50	2	16	4	140
	50	3	16	4	113
	50	4	16	8	313
	60	5	5	41	2624
	50	6	32	6	270
	50	7	32	6	455
	50	8	8	73	115
	50	9	114	46	244
	50	10	32	6	408
PAF44	50	11	32	2	543
	50	12	32	2	543
	50	13	32	2	543
	50	14	32	2	543
	50	15	32	2	543
	50	16	32	2	543
	50	17	32	2	543
	50	18	32	2	543
	50	19	32	2	543
	50	20	32	2	543

RESUMO ACO CA 50-60			
ACO	BIT (mm)	COMPR (m)	PESO (kg)
60	5	521	80
50	6.3	245	60
50	8	289	114
50	12.5	101	98
50	16	249	393
50	20	24	60
50	25	178	685
50	32	168	1062
Peso Total			80 kgf
Peso Total			2472 kgf

PROJETOS COMPLEMENTARES EM REFERÊNCIA:

- 1- FORMA DO NÍVEL +1037,25 - TORRE 1: DES. EPRO/SOMATTOS: 310-AURAE-EST-EX-0002-TRAVT1-R02;
- 2- FORMA DO 3o.SUBSOLO - TORRE 1: DES. EPRO/SOMATTOS: 310-AURAE-EST-EX-0005-3SUBS1-R05;
- 3- FORMA DO 2o.SUBSOLO - TORRE 1: DES. EPRO/SOMATTOS: 310-AURAE-EST-EX-0006-3SUBS1-R01;
- 4- FORMA DO 1o.SUBSOLO - TORRE 1: DES. EPRO/SOMATTOS: 310-AURAE-EST-EX-0007-3SUBS1-R01;
- 5- FORMA DO 1o.PAVIMENTO - TORRE 1: DES. EPRO/SOMATTOS: 310-AURAE-EST-EX-0008-PILOT1-R01;
- 6- FORMA DO NÍVEL +1037,25 - TORRE 2: DES. EPRO/SOMATTOS: 310-AURAE-EST-EX-0010-TRAVT2-R04;

NORMAS ATENDIDAS

- 1- NBR 6118/2023: PROJETO DE ESTRUTURAS DE CONCRETO;
- 2- NBR 14931/2004: EXECUÇÃO DE ESTRUTURAS DE CONCRETO - PROCEDIMENTO;
- 3- NBR 5674/2024: MANUTENÇÃO DE EDIFICAÇÕES-REQUISITOS PARA O SISTEMA DE GESTÃO E MANUTENÇÃO;
- 4- NBR 6120/2019: AÇÕES PARA CÁLCULO DE ESTRUTURA DE EDIFICAÇÕES;
- 5- NBR 6122/2019/EmL:2022: PROJETO E EXECUÇÃO DE FUNDAÇÕES;
- 6- NBR 15575/2024: EDIFICAÇÕES HABITACIONAIS - DESEMPENHO;
- 7- NBR 6123/2023: FORÇAS DEVIDAS AO VENTO EM EDIFICAÇÕES;
- 8- NBR 15200/2024: PROJETO DE ESTRUTURAS DE CONCRETO EM SITUAÇÃO DE INCÊNDIO;
- 9- NBR 17170/2022: EDIFICAÇÕES - GARANTIAS - PRAZOS RECOMENDADOS E DIRETRIZES;

NOTAS GERAIS:

- 1- COTAS EM CENTÍMETRO, NÍVEIS EM METRO;
- 2- CONCRETO ESTRUTURAL:
 - FCK >= 40,0 MPa;
 - FATOR ÁGUA/CEMENTO (A/C) <= 0,60
 - CONSUMO MÍNIMO DE CIMENTO = 280 kg/m3;
 - TEMPO DE CURA, CONFORME CONDIÇÕES CLIMÁTICAS, MÍNIMO DE 7 (SETE) DIAS;
- 3- MÓDULO DE ELASTICIDADE INICIAL DO CONCRETO NBR 6118/2023;
 $E_{ci} = 5600 \sqrt{FCK}$ (DADOS EM MPa) - $\alpha_E=1,0$ PARA GRANITO E GNATISSE;
PARA FCK >= 40,0 MPa - $E_{ci} = 33130$ MPa;
- 4- COEFICIENTE = 2,5 CM;
- 5- AÇOS CA 50 E CA 60;

05			
04			
03			
02			
01			
00	EMIÇÃO INICIAL	Rosana	13/10/25
Nº	HISTÓRICO	REVISÕES	RESPONSÁVEL DATA

PROPRIETÁRIO:
SOMATTOS PATRIMAR Q.40 EMPREND.IMOBILIÁRIOS SPE LTDA
CNPJ: 42.306.807/0001-05
AUTOR DO PROJETO:
TORRES WERANDA ARQUITETURA E CONSULTORIA LTDA
CAU: 8447-6
RESPONSÁVEL TÉCNICO EXECUÇÃO:
BERNARDO IMPELLIZIERI SÁ MATTOS
CREA: 82679/D MG
RESPONSÁVEL TÉCNICO PROJ. EXECUTIVO:
EPRO ENGENHARIA DE PROJETOS E CONSULTORIA S/C LTDA
CREA: 6154/MG
ENGENHEIRO COLABORADOR:
LUIZ RENATO DE LIMA
CREA: 26927/D

EMPREENHIMENTO:			
C000160: 310 - AURA - TORRE 1			
LOCAL: RUA CEL. GABRIEL FELIPE FARIA, VILA DA SERRA - NOVA LIMA - MG		BAIRRO: JARDINAVES	
PROJETO: PROJETO EXECUTIVO ESTRUTURAL		DATA 1a. EMISSÃO: 13/10/2025	
CONTEÚDO: ARMAÇÃO DOS PILARES DA ÁREA FRONTAL (TORRE 1) - 2a. PARTE		REVISÃO: R00	
ARQUIVO: 310-AURAT1-EST-EX-0131-ARMPIL-R00		ESCALA: INDICADA	
		FOLHA: 131/	